
THIS PLAT IS A CORRECT REPRESENTATION OF THE LANDS SURVEYED; HOWEVER A NORTH CAROLINA LICENSED ATTORNEY SHOULD BE CONSULTED CONCERNING CORRECT OWNERSHIP, WIDTH AND LOCATION OF ANY EASEMENTS, ANY CEMETERIES, OR FAMILY BURIAL GROUNDS NOT SHOWN ON RECORDED MAPS OR DEEDS MADE AVAILABLE TO THIS SURVEYOR BY THE RECENT OWNERS AT THE TIME OF THIS SURVEY AND OTHER TITLE QUESTIONS REVEALED BY TITLE EXAMINATION. NO RESPONSIBILITY OF ANY NATURE IS ASSUMED BY THIS SURVEYOR FOR ANY CONDITIONS WHICH MAY EXIST BUT ARE UNKNOWN, SUCH AS: CEMETERIES, FAMILY BURIAL GROUNDS, TOXIC OR HAZARDOUS WASTE MATERIAL, UNDERGROUND TANKS, ETC.

SEPTIC NOTE:
REGARDING THE WELL AND SEPTIC EVALUATION, JOHNSTON COUNTY ENVIROMENTAL HEALTH NO LONGER EVALUATES PROPRTIES PROPOSED AS MINOR SUBDIVISION MAPS OR EXEMPT MAPS PRIOR TO RECORDING UNLESS A WELL OR SEPTIC PERMIT HAS BEEN OBTAINED FOR THIS PROPERTY, THEN THE SUITABILITY OF THIS SITE FOR WELL OR SEPTIC SYSTEMS IS NOT CONFIRMED. CONSULT A LICENSED SOIL SCIENTIST IF ANY INITIAL SOIL EVALUATION IS NEEDED ON THE PROPERTY. CONSULT A LICENSED WELL OR SEPTIC INSTALLER FOR ASSISTANCE WITH LOCATING EXISTING SYSTEMS OR CONFLICTS ON SITE.

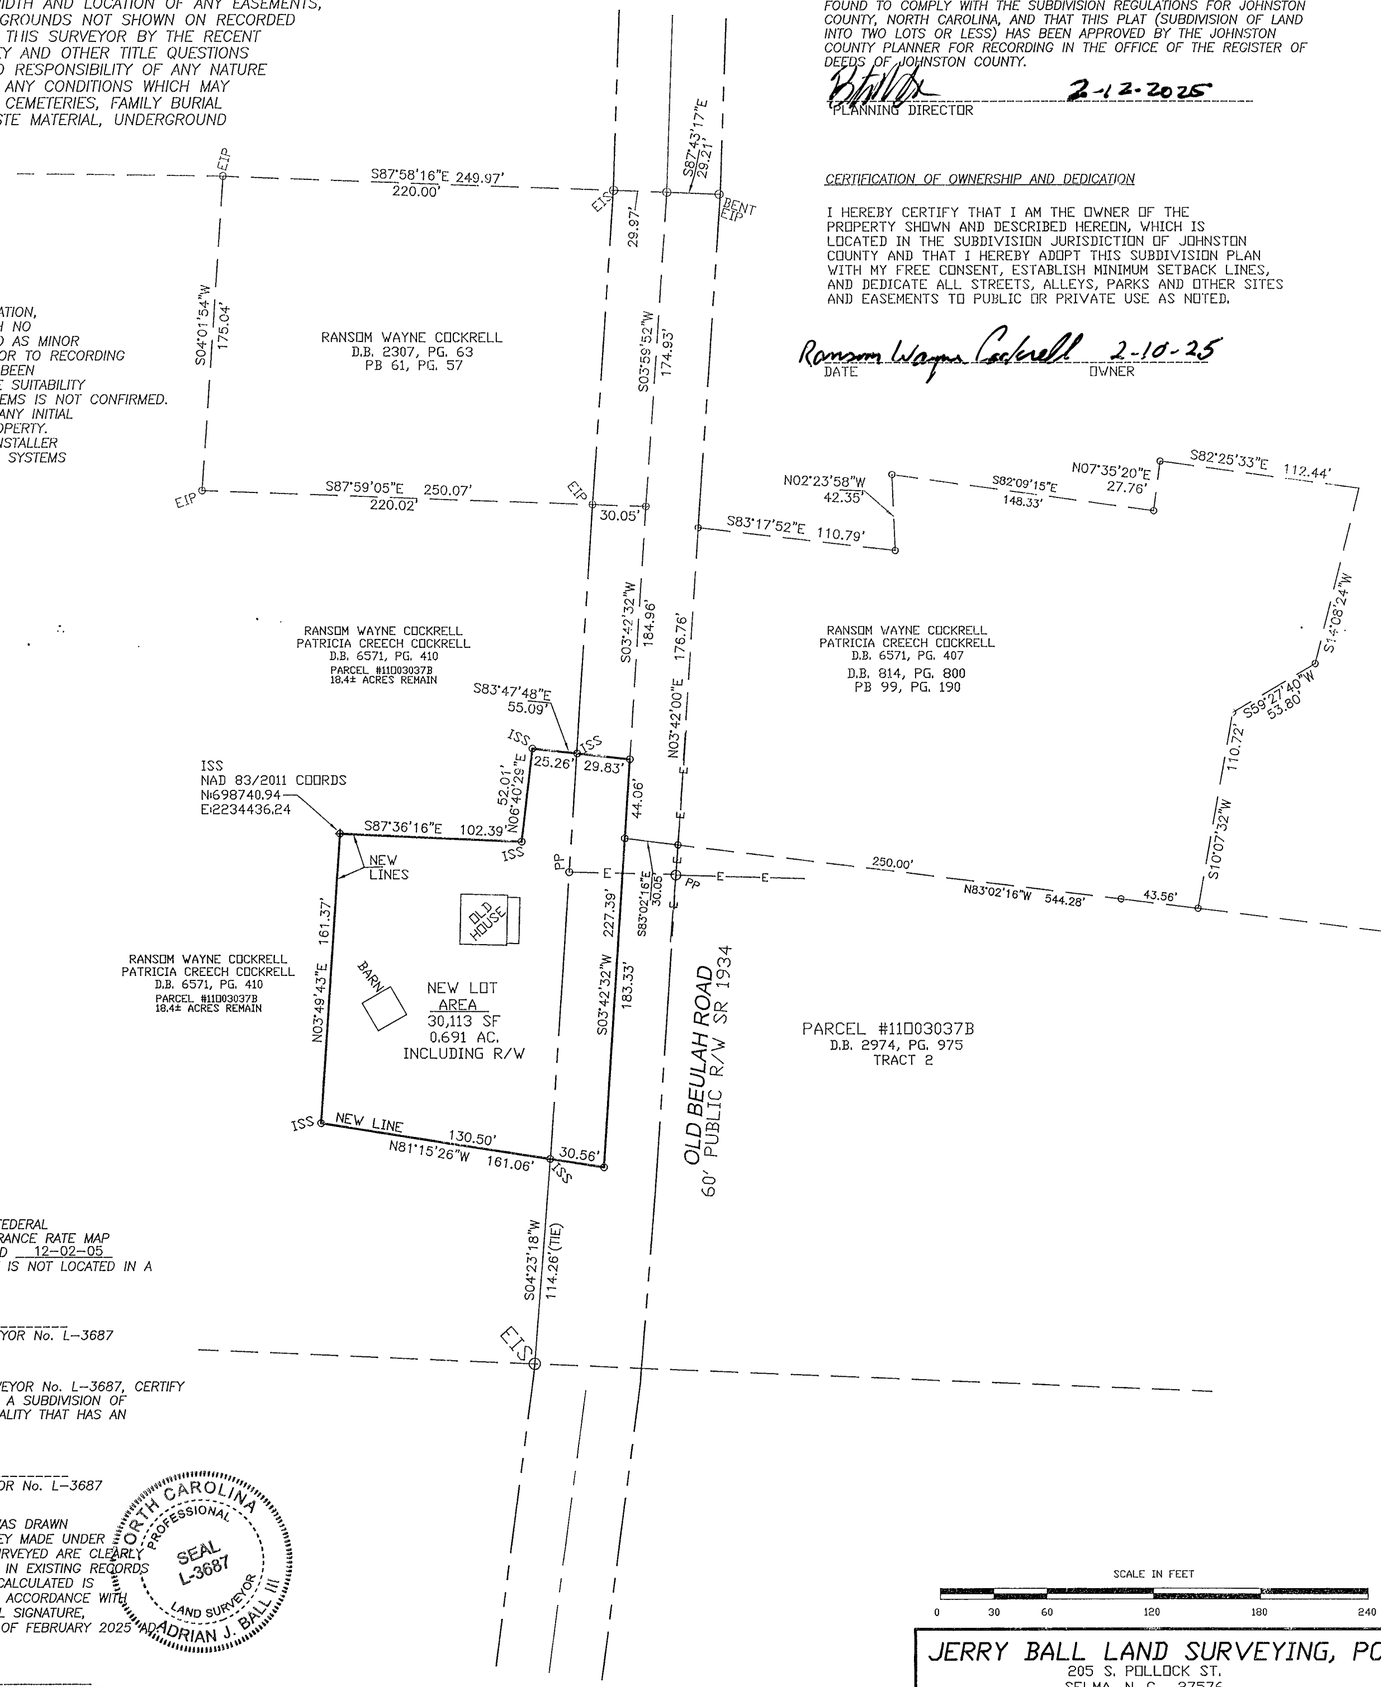

PLANNING DIRECTOR ENDORSEMENT


I HEREBY CERTIFY THAT THE SUBDIVISION PLAT SHOWN HEREIN HAS BEEN FOUND TO COMPLY WITH THE SUBDIVISION REGULATIONS FOR JOHNSTON COUNTY, NORTH CAROLINA, AND THAT THIS PLAT (SUBDIVISION OF LAND INTO TWO LOTS OR LESS) HAS BEEN APPROVED BY THE JOHNSTON COUNTY PLANNER FOR RECORDING IN THE OFFICE OF THE REGISTER OF DEEDS OF JOHNSTON COUNTY.

PLANNING DIRECTOR — 2-12-2025

CERTIFICATION OF OWNERSHIP AND DEDICATION

I HEREBY CERTIFY THAT I AM THE OWNER OF THE PROPERTY SHOWN AND DESCRIBED HEREON, WHICH IS LOCATED IN THE SUBDIVISION JURISDICTION OF JOHNSTON COUNTY AND THAT I HEREBY ADOPT THIS SUBDIVISION PLAN WITH MY FREE CONSENT, ESTABLISH MINIMUM SETBACK LINES, AND DEDICATE ALL STREETS, ALLEYS, PARKS AND OTHER SITES AND EASEMENTS TO PUBLIC OR PRIVATE USE AS NOTED.

Ransom Wayne Cockrell — 2-10-25
DATE — OWNER

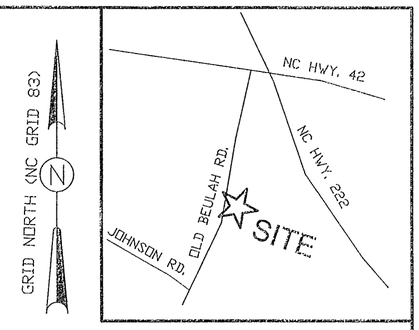

VICINITY MAP - NO SCALE

LEGEND

N&C	NAIL AND CAP
PKS	PK NAIL SET
EIP	EXISTING IRON PIPE
EIS	EXISTING IRON STAKE
IPS	IRON PIPE SET
PUP	POINT UNDER PAVEMENT
R/W	RIGHT-OF-WAY
CL	CENTERLINE

REF: BEING A MINOR SUBDIVISON OF THE PROPERTY SHOWN AND DESCRIBED IN D.B. 6571, PG. 410 OF THE JOHNSTON COUNTY REGISTER OF DEEDS OFFICE

PLAT REFERENCES: PB 61, PG. 57
PB 55, PG. 339
PB 78, PG. 242
PB 93, PG. 229
PB 99, PG. 190

Filed in JOHNSTON, NC
Filed 02/14/2025 01:49:58 PM
CRAIG OLIVE, Register of Deeds
Dep/Asst ebyrd
PLAT B: 102 P: 462

THIS IS TO CERTIFY THAT I HAVE CONSULTED FEDERAL EMERGENCY MANAGEMENT AGENCY FLOOD INSURANCE RATE MAP COMMUNITY PANEL No. 3720263900 J DATED 12-02-05 AND FOUND THAT NO PART OF THIS PROPERTY IS NOT LOCATED IN A SPECIAL FLOOD HAZARD AREA.

ADRIAN J. BALL III, PROFESSIONAL LAND SURVEYOR No. L-3687

I, ADRIAN J. BALL III, PROFESSIONAL LAND SURVEYOR No. L-3687, CERTIFY THAT THIS PLAT IS OF A SURVEY THAT CREATES A SUBDIVISION OF LAND WITHIN THE AREA OF COUNTY OR MUNICIPALITY THAT HAS AN ORDINANCE THAT REGULATES PARCELS OF LAND.

ADRIAN J. BALL III, PROFESSIONAL LAND SURVEYOR No. L-3687

I, ADRIAN J. BALL III, CERTIFY THAT THIS PLAT WAS DRAWN UNDER MY SUPERVISION FROM AN ACTUAL SURVEY MADE UNDER MY SUPERVISION; THAT THE BOUNDARIES NOT SURVEYED ARE CLEARLY INDICATED AS DRAWN FROM INFORMATION FOUND IN EXISTING RECORDS AS NOTED; THAT THE RATION OF PRECISION AS CALCULATED IS 1 : 10000+; THAT THIS PLAT WAS PREPARED IN ACCORDANCE WITH G.S. 47-30 AS AMENDED. WITNESS MY ORIGINAL SIGNATURE, REGISTRATION NUMBER AND SEAL THIS 6TH DAY OF FEBRUARY 2025 A.D.

NORTH CAROLINA PROFESSIONAL SEAL L-3687 LAND SURVEYOR ADRIAN J. BALL III

ADRIAN J. BALL III, PROFESSIONAL LAND SURVEYOR No. L-3687

STATE OF NORTH CAROLINA
COUNTY OF JOHNSTON

I, Jodie R. H. Gay, REVIEW OFFICER OF JOHNSTON COUNTY, CERTIFY THAT THE MAP OR PLAT TO WHICH THIS CERTIFICATION IS AFFIXED MEETS ALL STATUTORY REQUIREMENTS FOR RECORDING.

02-12-2025 — Jodie R. H. Gay
DATE — REVIEW OFFICER

SCALE IN FEET
0 30 60 120 180 240

JERRY BALL LAND SURVEYING, PC
205 S. POLLOCK ST.
SELMA, N. C. 27576
(919) 965-0077

OWNER: PATRICIA CREECH COCKRELL
WAYNE COCKRELL
10720 OLD BEULAH RD.
KENLY, NC

CORP. #L-3000

MINOR SUBDIVISION FOR
GREGORY WAYNE COCKRELL
AND
CRYSTAL W. COCKRELL
ON THE LANDS OF
RANSOM WAYNE COCKRELL
AND
PATRICIA CREECH COCKRELL

O'NEALS TOWNSHIP — JOHNSTON COUNTY
NORTH CAROLINA
SCALE: 1" = 60' — DWN. BY: AJB
DATE: 02-06-25

COCKRELLWAYNE