

BOM 2005, PG. 529 & 530

60 0 30 60 120

(IN FEET)
1 inch = 60 ft.
GRAPHIC SCALE

N.C. HIGHWAY NO. 50 ~ CREEDMOOR ROAD
VARIABLE WIDTH PUBLIC R/W

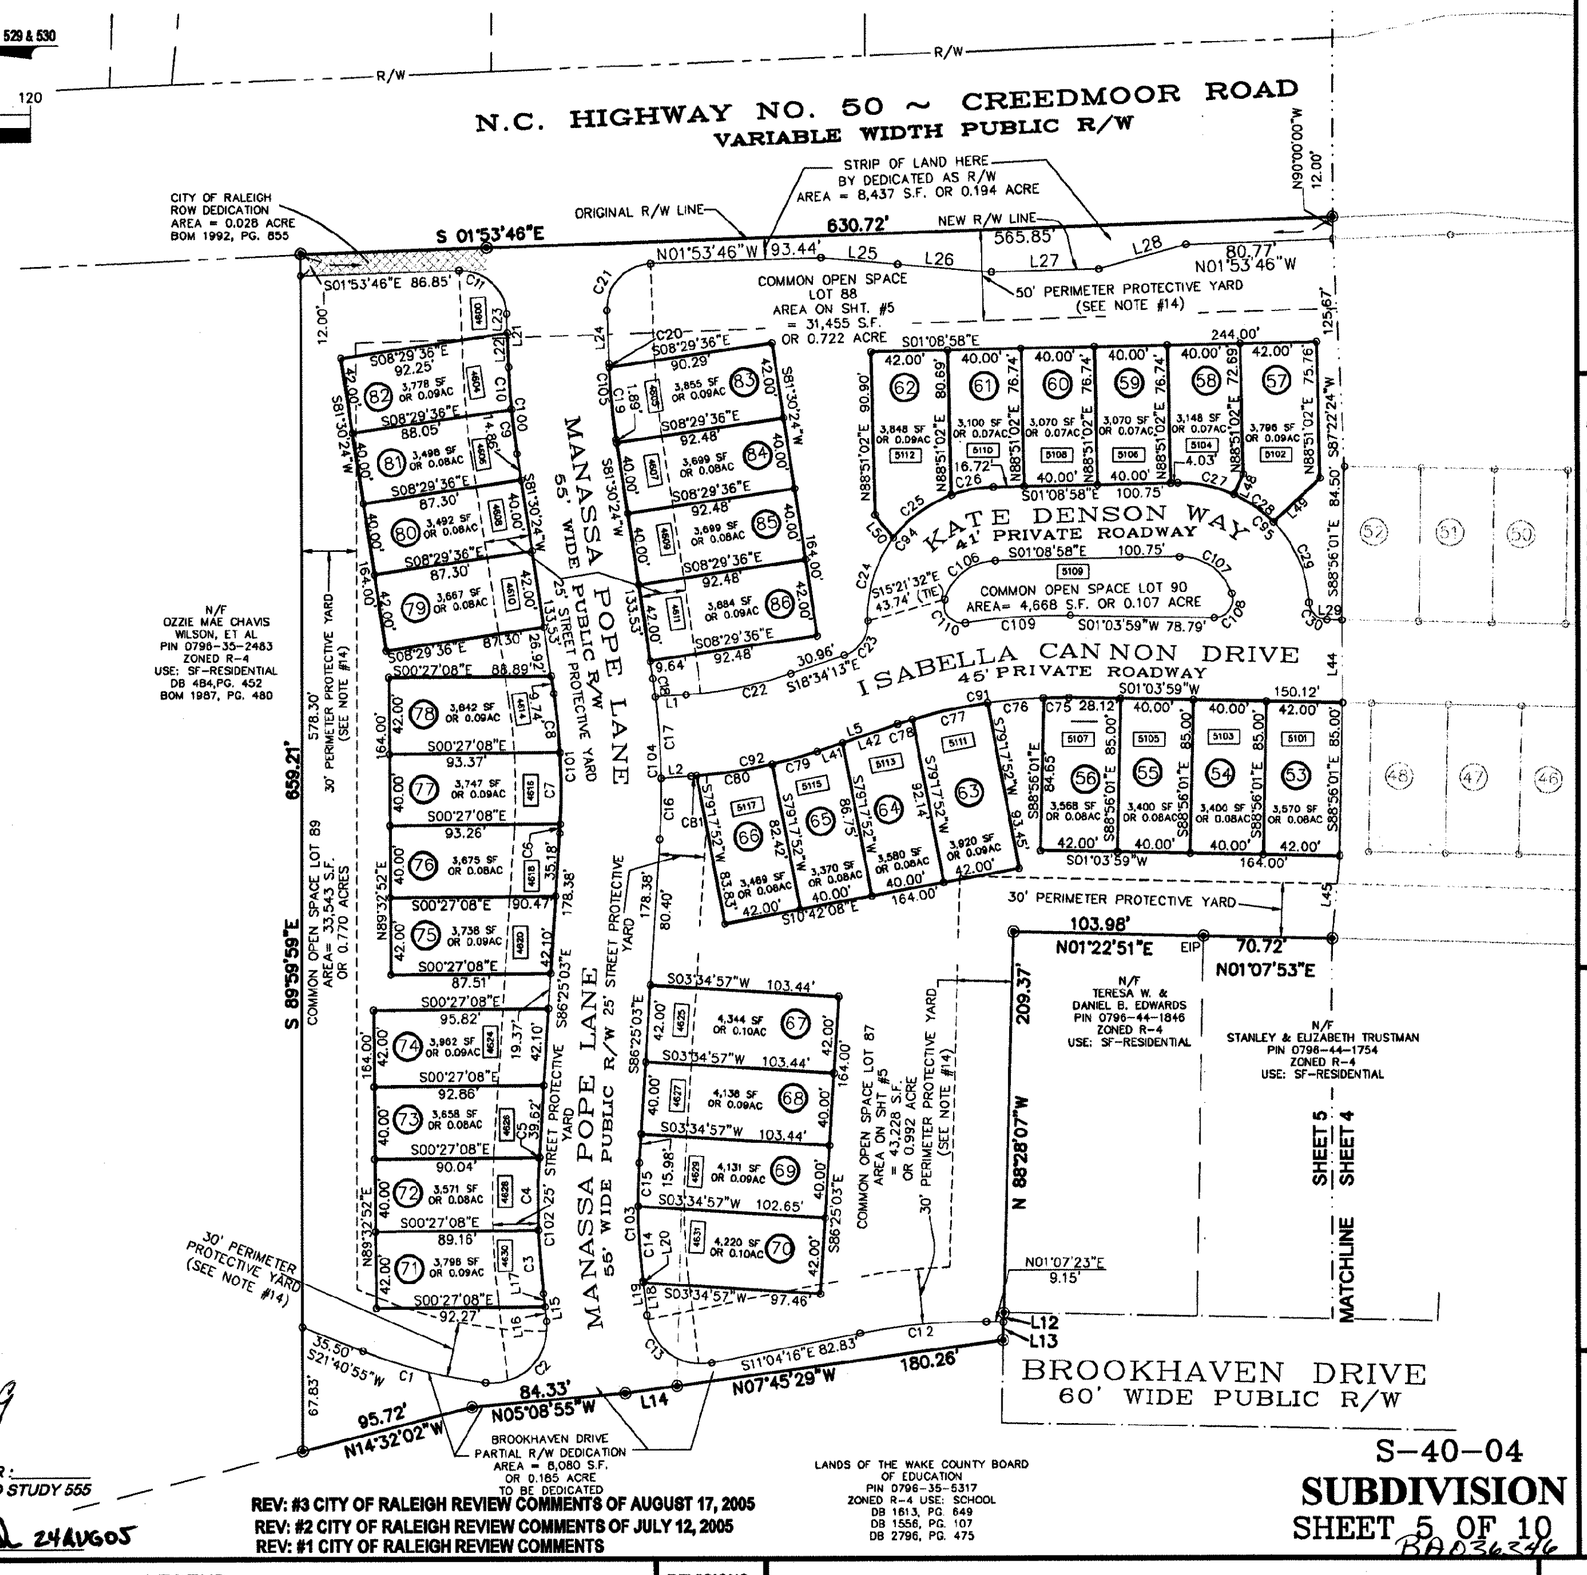

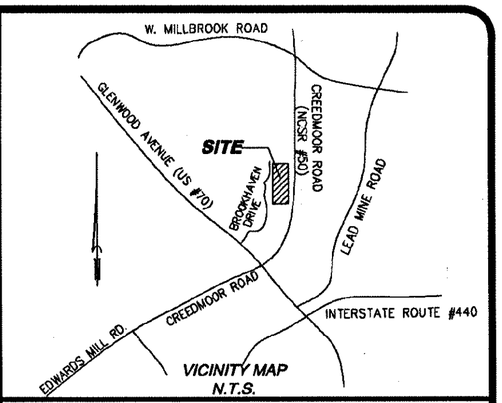

I, MARK J. OROPALLO, PLS NO. L-4188, CERTIFY TO THE FOLLOWING:

THE SURVEY CREATES A SUBDIVISION OF LAND WITHIN THE AREA OF A COUNTY OR MUNICIPALITY THAT HAS AN ORDINANCE THAT REGULATES PARCELS OF LAND.

I, MARK J. OROPALLO, PLS NO. L-4188, CERTIFY THAT THIS MAP WAS DRAWN FROM AN ACTUAL SURVEY MADE UNDER MY SUPERVISION; THAT THE DEED DESCRIPTION(S) AND PLAT(S) FOR THIS PROPERTY IS (ARE) LISTED HEREON UNDER "REFERENCES"; THAT THE BOUNDARIES NOT SURVEYED ARE CLEARLY INDICATED IN A BROKEN LINETYPE, AND ARE DRAWN FROM INFORMATION SOURCES LISTED UNDER "REFERENCES"; THAT THE RATIO OF PRECISION AS CALCULATED IS 1:10000 OR GREATER, THAT THIS MAP WAS PREPARED IN ACCORDANCE WITH G.S.47-30 AS AMENDED. WITNESSED BY MY ORIGINAL SIGNATURE, LICENSE NUMBER AND SEAL THIS 17TH. DAY OF AUGUST, 2005.

NORTH CAROLINA PROFESSIONAL SEAL L-4188 LAND SURVEYOR MARK J. OROPALLO

MARK J. OROPALLO, PLS
PROFESSIONAL LAND SURVEYOR LIC. # L-4188

REFERENCES

DB	11199,	PG.	918	BOM	1952 PG. 94
DB	1112,	PG.	559	BOM	1992, PG. 855
DB	2796,	PG.	475	BOM	1987, PG. 480
DB	4114,	PG.	452	BOM	1980, PG. 548
DB	4114,	PG.	446	BOM	1955, PG. 110
DB	10708,	PG.	9	BOM	1978, PG. 443
DB	1556,	PG.	107	BOM	1959, PG. 227
DB	1631,	PG.	469	BOM	1998, PG. 1824
				BOM	1999, PG. 1412

WAKE COUNTY, NC 344
LAURA M RIDDICK
REGISTER OF DEEDS
PRESENTED & RECORDED ON
08/24/2005 AT 13:34:16

BOOK:BM2005 PAGE:01709

Book 2005 pg 1709

FLOOD PLAIN ORDINANCE
[ ] FEMA MAPPED AREA MAP NUMBER :_____
[X] OTHER: CITY OF RALEIGH FLOOD STUDY 555

APPROVED BY: John D Burbank 24AUG05

REV: #3 CITY OF RALEIGH REVIEW COMMENTS OF AUGUST 17, 2005
REV: #2 CITY OF RALEIGH REVIEW COMMENTS OF JULY 12, 2005
REV: #1 CITY OF RALEIGH REVIEW COMMENTS

S-40-04
SUBDIVISION
SHEET 5 OF 10
BA036246

OWNERS ADDRESS:
PULTE HOME CORPORATION
801 CORPORATE CENTER DRIVE
SUITE 118, RALEIGH N.C. 27607

PIN 0796-44-4054 0796-45-1061 0796-44-4878 0796-45-2245
TAX MAP # 0796.14
DRAWN BY: D.S.Z.
CHECKED BY: K.S.

LEGEND:

- EXISTING IRON PIPE
- IRON PIN SET
- MATHEMATICAL POINT
- EXISTING N.C. DOT R/W DISK
- NORTH CAROLINA RIGHT-OF-WAY CONCRETE MONUMENT
- CONTROL CORNER
- IPS IRON PIN SET
- 50' NEUSE RIVER BUFFER LINE
- 0000 STREET ADDRESS
- N.C.G.S. CONTROL MONUMENT
- DB DEED BOOK
- PG PAGE
- BOM BOOK OF MAPS
- EIR EXISTING IRON ROD
- R/W RIGHT OF WAY
- 50' NATURAL PROTECTIVE YARD
- 100 YEAR FLOOD PLAIN
- C.O.R. CITY OF RALEIGH
- EXISTING 20' & 10' C.O.R. SANITARY SEWER AND WATER LINE EASEMENTS HEREBY ABANDONED PER CITY COUNCIL RESOLUTION NUMBER 2005-595.
- NEW CITY OF RALEIGH WATER EASEMENT HEREBY DEDICATED

REVISIONS
#1 6/08/2005
#2 7/25/2005
#3 8/17/2005

SUBDIVISION PLAT AND RIGHT OF WAY DEDICATION FOR "COPPER RIDGE TOWNHOMES"

CITY:	COUNTY:	STATE:	DATE:	DRAWING:
RALEIGH	WAKE	NORTH CAROLINA	APRIL 28, 2005	99-08-16

SURVEYED by

MSS LAND CONSULTANTS
5540 McNeely Dr. (Suite 101) Raleigh, NC 27612
Phone (919) 510-4464
Fax (919) 510-9102
Email: oropallomj@mssland.com

"Committed to Total Quality Service"

O:/PULTE/99-08-16/DWG/COPPERSUBD.DWG