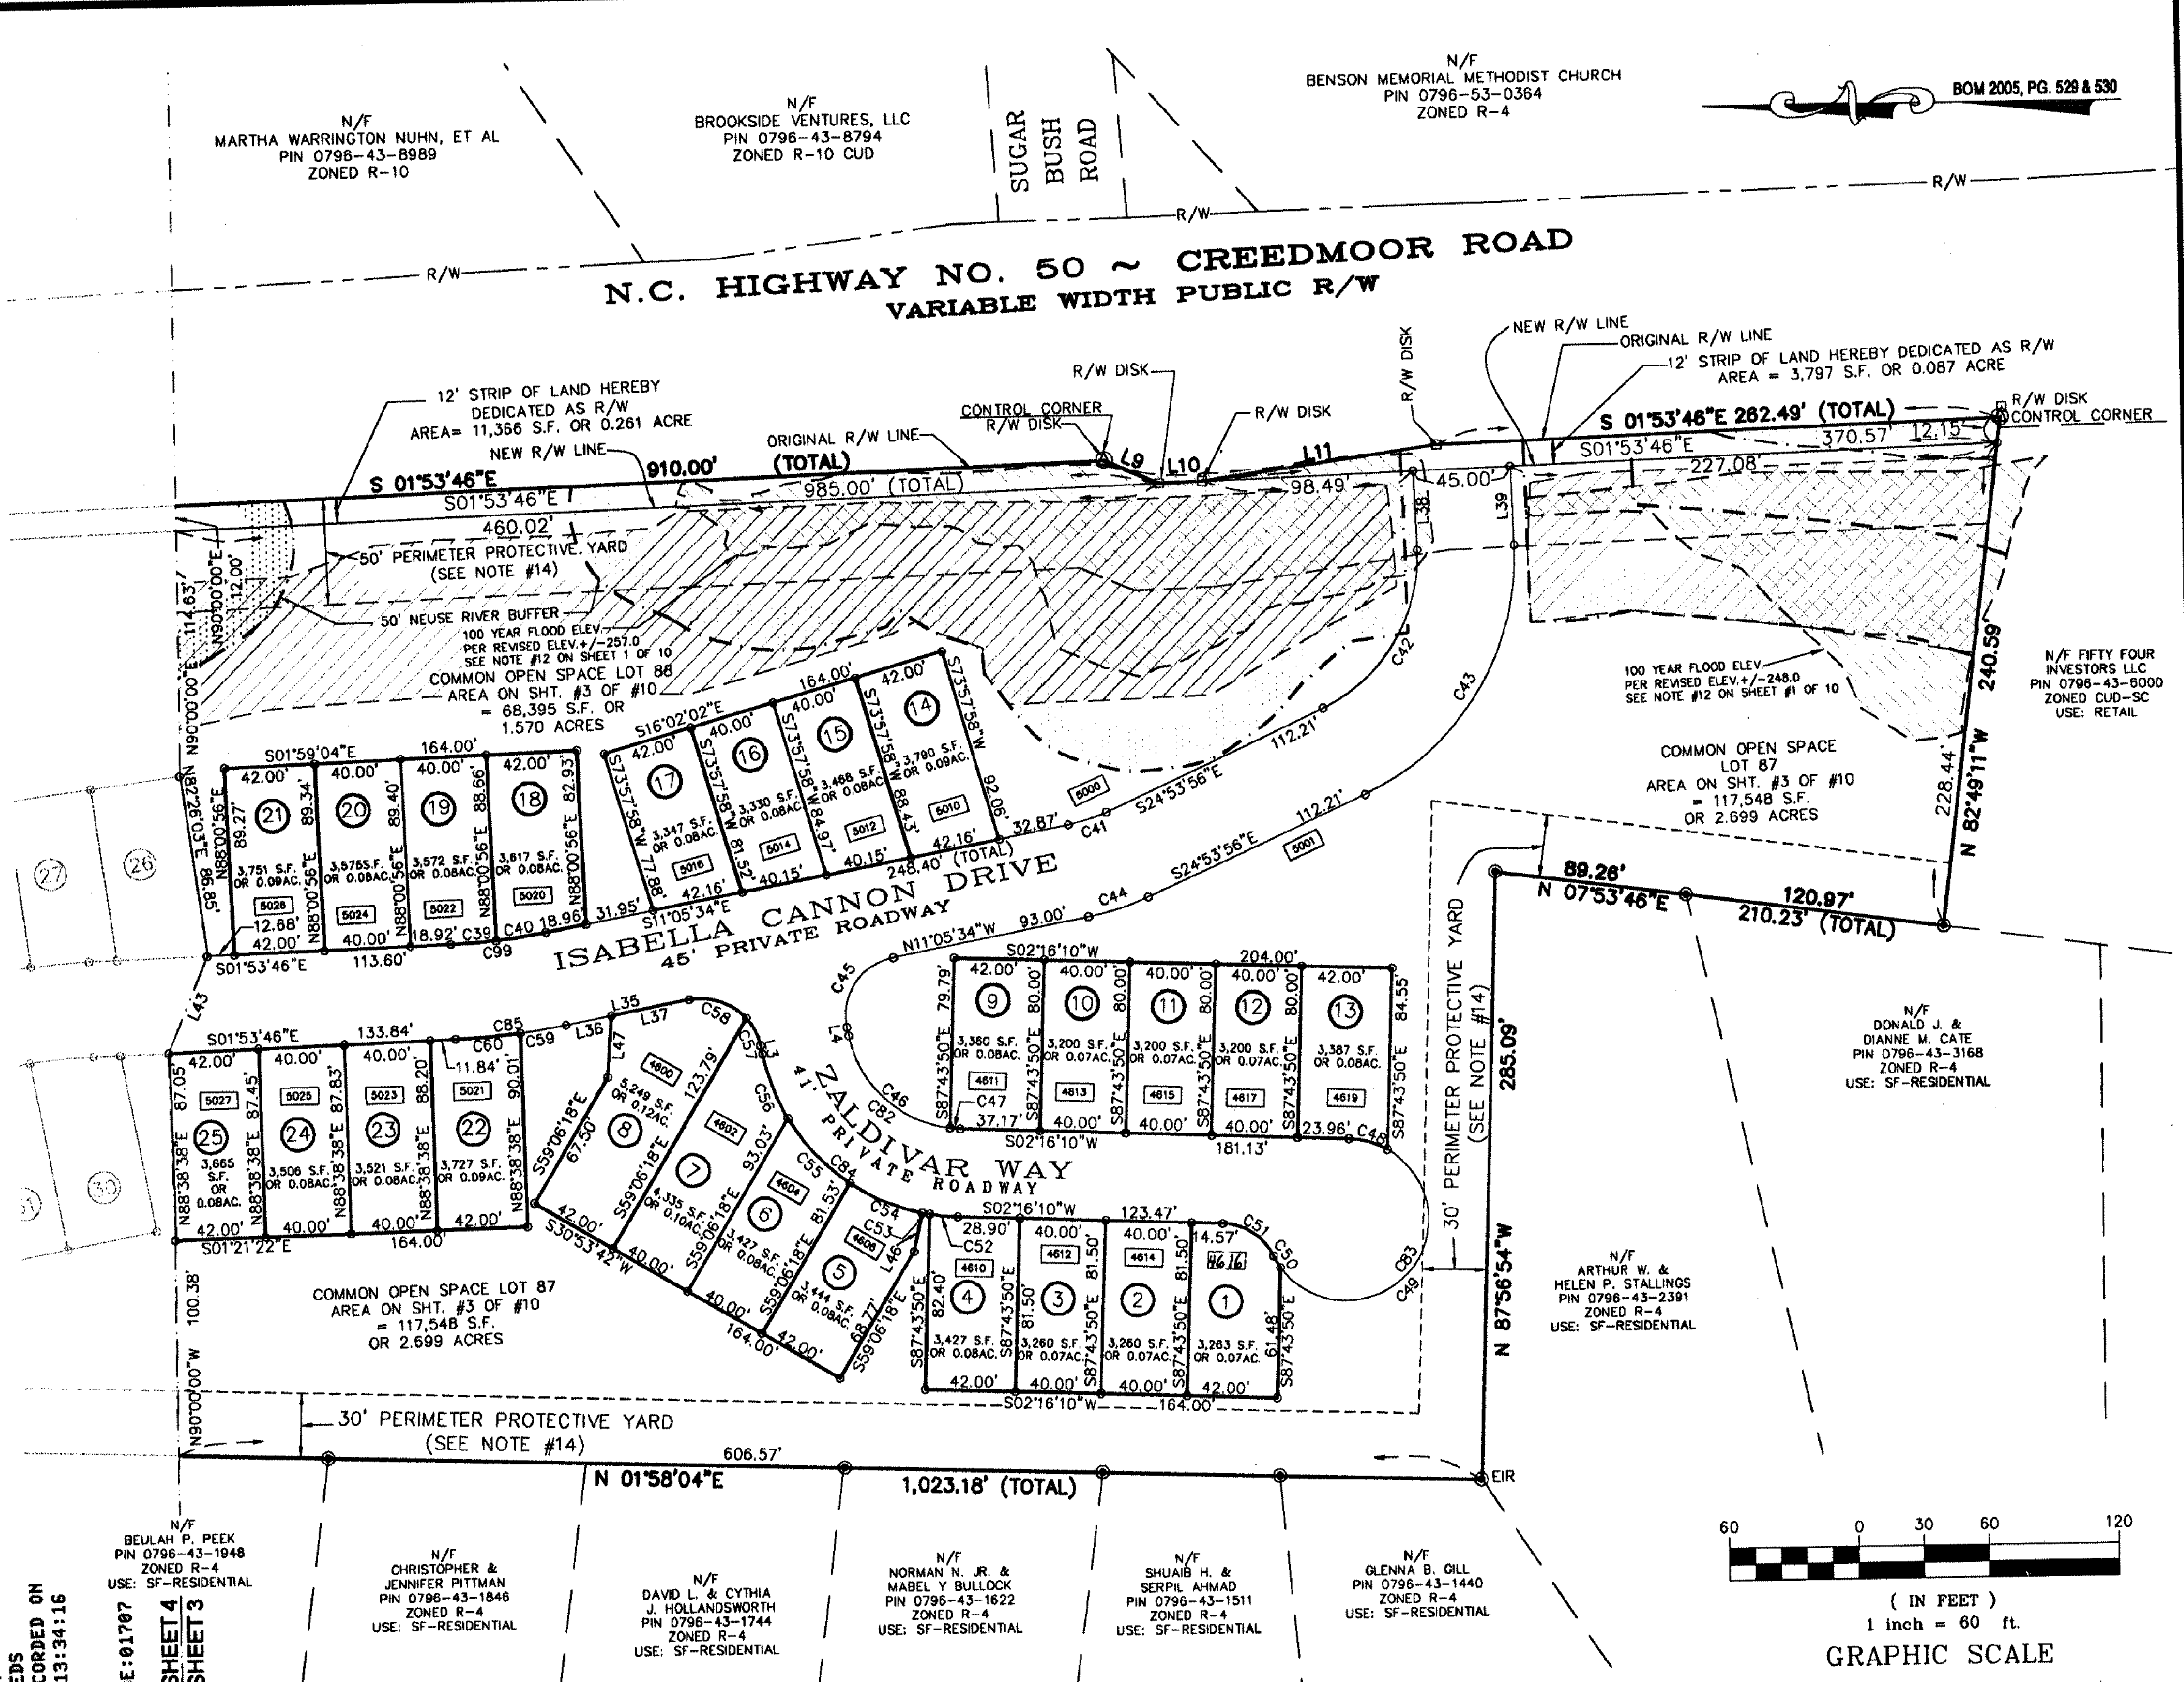
N/F
MARTHA WARRINGTON NUHN, ET AL
PIN 0796-43-8989
ZONED R-10
N/F
BROOKSIDE VENTURES, LLC
PIN 0796-43-8794
ZONED R-10 CUD
SUGAR BUSH ROAD
N/F
BENSON MEMORIAL METHODIST CHURCH
PIN 0796-53-0364
ZONED R-4
BOM 2005, PG. 529 & 530
R/W
N.C. HIGHWAY NO. 50 ~ CREEDMOOR ROAD
VARIABLE WIDTH PUBLIC R/W
12' STRIP OF LAND HEREBY DEDICATED AS R/W AREA= 11,356 S.F. OR 0.261 ACRE
NEW R/W LINE
S 01°53'46"E 910.00' (TOTAL)
S01°53'46"E
985.00' (TOTAL)
460.02'
ORIGINAL R/W LINE
CONTROL CORNER R/W DISK
R/W DISK
L9
L10
L11
98.49'
L38
45.00'
L39
R/W DISK
NEW R/W LINE
ORIGINAL R/W LINE
12' STRIP OF LAND HEREBY DEDICATED AS R/W AREA = 3,797 S.F. OR 0.087 ACRE
S 01°53'46"E 282.49' (TOTAL)
370.57'
12.15'
S01°53'46"E
227.08'
R/W DISK CONTROL CORNER
50' PERIMETER PROTECTIVE YARD (SEE NOTE #14)
50' NEUSE RIVER BUFFER
100 YEAR FLOOD ELEV. PER REVISED ELEV.+/-257.0 SEE NOTE #12 ON SHEET 1 OF 10
COMMON OPEN SPACE LOT 88 AREA ON SHT. #3 OF #10 = 68,395 S.F. OR 1.570 ACRES
100 YEAR FLOOD ELEV. PER REVISED ELEV.+/-248.0 SEE NOTE #12 ON SHEET #1 OF 10
COMMON OPEN SPACE LOT 87 AREA ON SHT. #3 OF #10 = 117,548 S.F. OR 2.699 ACRES
N/F FIFTY FOUR INVESTORS LLC
PIN 0796-43-6000
ZONED CUD-SC
USE: RETAIL
240.59'
228.44'
N 82°49'11"W
C42
C43
ISABELLA CANNON DRIVE
45' PRIVATE ROADWAY
ZALDIVAR WAY
41' PRIVATE ROADWAY
89.26'
N 07°53'46"E
120.97'
210.23' (TOTAL)
N/F
DONALD J. & DIANNE M. CATE
PIN 0796-43-3168
ZONED R-4
USE: SF-RESIDENTIAL
30' PERIMETER PROTECTIVE YARD (SEE NOTE #14)
285.09'
N 87°56'54"W
N/F
ARTHUR W. & HELEN P. STALLINGS
PIN 0796-43-2391
ZONED R-4
USE: SF-RESIDENTIAL
21
20
19
18
17
16
15
14
13
12
11
10
9
25
24
23
22
8
7
6
5
4
3
2
1
27
26
30
31
COMMON OPEN SPACE LOT 87 AREA ON SHT. #3 OF #10 = 117,548 S.F. OR 2.699 ACRES
30' PERIMETER PROTECTIVE YARD (SEE NOTE #14)
606.57'
N 01°58'04"E
1,023.18' (TOTAL)
EIR
N/F
BEULAH P. PEEK
PIN 0796-43-1948
ZONED R-4
USE: SF-RESIDENTIAL
N/F
CHRISTOPHER & JENNIFER PITTMAN
PIN 0796-43-1846
ZONED R-4
USE: SF-RESIDENTIAL
N/F
DAVID L. & CYTHIA J. HOLLANDSWORTH
PIN 0796-43-1744
ZONED R-4
USE: SF-RESIDENTIAL
N/F
NORMAN N. JR. & MABEL Y BULLOCK
PIN 0796-43-1622
ZONED R-4
USE: SF-RESIDENTIAL
N/F
SHUAIB H. & SERPIL AHMAD
PIN 0796-43-1511
ZONED R-4
USE: SF-RESIDENTIAL
N/F
GLENNA B. GILL
PIN 0796-43-1440
ZONED R-4
USE: SF-RESIDENTIAL
60 0 30 60 120
(IN FEET)
1 inch = 60 ft.
GRAPHIC SCALE


W. MILLBROOK ROAD
GLENWOOD AVENUE (US #70)
SITE
BROOKHAVEN DRIVE
CREEDMOOR ROAD (NCSR #50)
LEAD MINE ROAD
CREEDMOOR ROAD
INTERSTATE ROUTE #440
EDWARDS MILL RD.

VICINITY MAP
N.T.S.

I, MARK J. OROPALLO, PLS NO. L-4188, CERTIFY TO THE FOLLOWING:

THE SURVEY CREATES A SUBDIVISION OF LAND WITHIN THE AREA OF A COUNTY OR MUNICIPALITY THAT HAS AN ORDINANCE THAT REGULATES PARCELS OF LAND.

I, MARK J. OROPALLO, PLS NO. L-4188, CERTIFY THAT THIS MAP WAS DRAWN FROM AN ACTUAL SURVEY MADE UNDER MY SUPERVISION; THAT THE DEED DESCRIPTION(S) AND PLAT(S) FOR THIS PROPERTY IS (ARE) LISTED HEREON UNDER "REFERENCES"; THAT THE BOUNDARIES NOT SURVEYED ARE CLEARLY INDICATED IN A BROKEN LINETYPE, AND ARE DRAWN FROM INFORMATION SOURCES LISTED UNDER "REFERENCES"; THAT THE RATIO OF PRECISION AS CALCULATED IS 1:10000 OR GREATER, THAT THIS MAP WAS PREPARED IN ACCORDANCE WITH G.S.47-30 AS AMENDED. WITNESSED BY MY ORIGINAL SIGNATURE, LICENSE NUMBER AND SEAL THIS 17TH. DAY OF AUGUST, 2005.

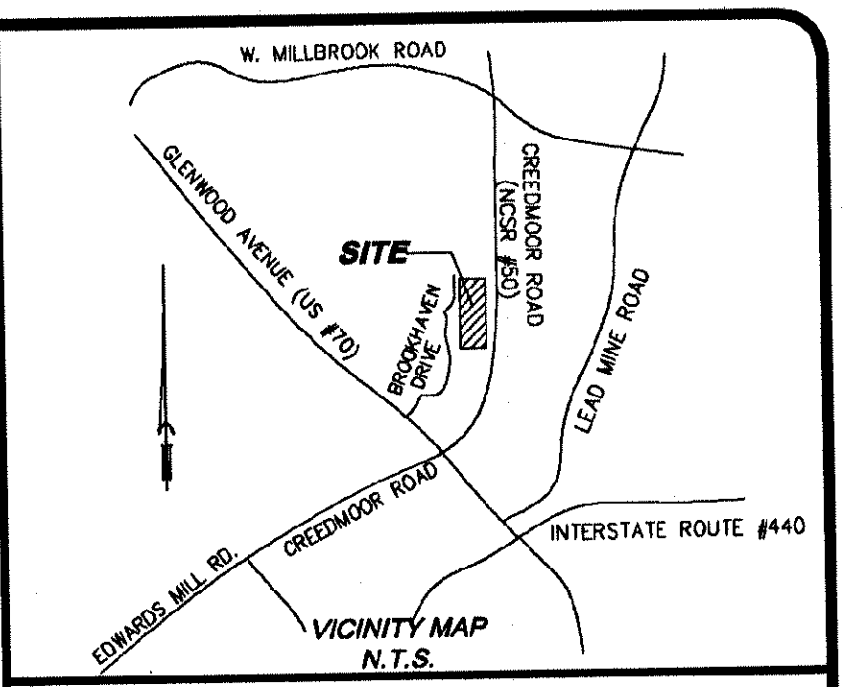L-4188
MARK J. OROPALLO

MARK J. OROPALLO, PLS
PROFESSIONAL LAND SURVEYOR LIC. # L-4188

REFERENCES

DB	11199,	PG.	918	BOM	1952	PG.	94
DB	1112,	PG.	559	BOM	1992,	PG.	855
DB	2796,	PG.	475	BOM	1987,	PG.	480
DB	4114,	PG.	452	BOM	1980,	PG.	548
DB	4114,	PG.	446	BOM	1955,	PG.	110
DB	10708,	PG.	9	BOM	1978,	PG.	443
DB	1556,	PG.	107	BOM	1959,	PG.	227
DB	1631,	PG.	469	BOM	1998,	PG.	1824
				BOM	1999,	PG.	1412

WAKE COUNTY, NC 342
LAURA M RIDDICK
REGISTER OF DEEDS
PRESENTED & RECORDED ON
08/24/2005 AT 13:34:16

BOOK:BM2005 PAGE:01707

MATCHLINE SHEET 4 | SHEET 3

FLOOD PLAIN ORDINANCE
[ ] FEMA MAPPED AREA MAP NUMBER : ____
[X] OTHER: CITY OF RALEIGH FLOOD STUDY 555

APPROVED BY: John D Bunker 24AUG05

S-40-04
SUBDIVISION
SHEET 3 OF 10
RA036376

REV: #3 CITY OF RALEIGH REVIEW COMMENTS OF AUGUST 17, 2005
REV: #2 CITY OF RALEIGH REVIEW COMMENTS OF JULY 12, 2005
REV: #1 CITY OF RALEIGH REVIEW COMMENTS

OWNERS ADDRESS:
PULTE HOME CORPORATION
801 CORPORATE CENTER DRIVE
SUITE 118, RALEIGH N.C. 27607

PIN	0796-44-4054 0796-45-1061 0796-44-4876 0796-45-2245
TAX MAP #	0796.14
DRAWN BY:	KS
CHECKED BY:	MJO

LEGEND:

◉	EXISTING IRON PIPE
○	IRON PIN SET
△	MATHEMATICAL POINT
⊡	EXISTING N.C. DOT R/W DISK
■	NORTH CAROLINA RIGHT-OF-WAY CONCRETE MONUMENT
⊚	CONTROL CORNER
IPS	IRON PIN SET
▒	50' NEUSE RIVER BUFFER LINE
0000	STREET ADDRESS
▲	N.C.G.S. CONTROL MONUMENT
DB	DEED BOOK
PG	PAGE
BOM	BOOK OF MAPS
EIR	EXISTING IRON ROD
R/W	RIGHT OF WAY
▨	50' NATURAL PROTECTIVE YARD
▨	100 YEAR FLOOD PLAIN
C.O.R.	CITY OF RALEIGH
▒	EXISTING 20' & 10' C.O.R. SANITARY SEWER AND WATER LINE EASEMENTS HEREBY ABANDONED PER CITY COUNCIL RESOLUTION NUMBER 2005-595.
▨	NEW CITY OF RALEIGH WATER EASEMENT HEREBY DEDICATED

Book 2005 pg 1707

REVISIONS
#1 6/08/2005
#2 7/25/2005
#3 8/17/2005

SUBDIVISION PLAT AND RIGHT OF WAY DEDICATION FOR "COPPER RIDGE TOWNHOMES"

	COUNTY:	STATE:	DATE:	DRAWING:
RALEIGH	WAKE	NORTH CAROLINA	APRIL 28, 2005	99-08-16

SURVEYED by

MSS LAND CONSULTANTS
5540 McNeely Dr.
(Suite 101)
Raleigh, NC 27612
Phone (919) 510-4464
Fax (919) 510-9102
Email: oropallomj@mssland.com

"Committed to Total Quality Service"

O:/PULTE/99-08-16/DWG/COPPERSUBD.DWG

O:_PULTE\99-08-16\dwg\coppersubd.DWG, layout, 08/17/2005 04:43:02 PM, zmed