BOM 2005, PG. 529 & 530

60 0 30 60 120

(IN FEET)
1 inch = 60 ft.
GRAPHIC SCALE

N/F
C/O SENTINEL REAL ESTATE CORP.
HAMILTON RIDGE APARTMENTS
PIN 0796-54-2586
ZONED R-10

TALL TIMBER DRIVE

N/F
MARTHA WARRINGTON NUHN, ET AL
PIN 0796-43-8989
ZONED R-10

R/W R/W R/W

N.C. HIGHWAY NO. 50 ~ CREEDMOOR ROAD
VARIABLE WIDTH PUBLIC R/W

12' STRIP OF LAND HERE BY DEDICATED AS R/W AREA= 8,437 S.F. OR 0.194 ACRE

12' STRIP OF LAND HERE BY DEDICATED AS R/W AREA= 11,366 S.F. OR 0.261 ACRE

ORIGINAL R/W LINE
NEW R/W LINE
S 01°53'46"E 910.00' (TOTAL)
S01°53'46"E 985.00' (TOTAL)
524.98'
N90°00'00"W 12.00'
N90°00'00"E 114.63'
N90°00'00"E 12.00'
S87°22'24"W 125.67'
N90°00'00"W 12.00'
L6 L7 L8
165.27' R/W DISK
S01°53'46"E 165.27' R/W DISK

50' PERIMETER PROTECTIVE YARD (SEE NOTE #14)

50' NEUSE RIVER BUFFER

50' NEUSE RIVER BUFFER

50' NEUSE RIVER BUFFER

COMMON OPEN SPACE LOT 88
AREA ON SHT. #4=
127,309 S.F.
OR 2.923 ACRES

S01°03'59"W 42.00' 84.50' 3,549SF OR 0.08AC 5072 (52)
S88°56'01"E 84.50' 3,380 SF OR 0.08AC 5070 (51)
S88°56'01"E 84.50' 3,380 SF OR 0.08AC 5068 (50)
S88°56'01"E 84.50' 3,564 SF OR 0.08AC 5066 (49)
S88°56'01"E 86.13'
164.00'
42.00' 40.00' 40.00' 42.00'
15.08' C31 C32 33.87' S14°00'33"W C33 29.63' S12°19'00"E C34 61.02' S01°03'59"W 63.43'
137.08' C96

S10°54'30"E 42.00' 3,323 SF OR 0.08AC 5044 (36) 2.41' C35
40.00' 3,277 SF OR 0.08AC 5042 (35) 13.81' C36
124.00' 42.00' 3,401 SF OR 0.08AC 5040 (34) 81.61' 15.09' 42.02' C97
S79°05'30"W 75.61'
S79°05'30"W 81.36'
S79°05'30"W 98.37'

S07°33'57"E 164.00'
42.00' 3,508 SF OR 0.08AC 5036 (29) 42.16' 119.89' C98
40.00' 3,215 SF OR 0.07AC 5034 (28) 6.81' C37
40.00' 3,238 SF OR 0.07AC 5032 (27) 13.03' C38
42.00' 3,560 SF OR 0.08AC 5030 (26) 42.21' 55.24'
S82°26'03"W 98.85'
S01°53'46"E 35.00'

ISABELLA CANNON DRIVE
45' PRIVATE ROADWAY
ISABELLA CANNON DRIVE
45' PRIVATE ROADWAY

S01°03'59"W 42.00' 15.84' 3,470 SF OR 0.08AC 5071 (48) 82.62'
S88°56'01"E 40.00' 3,305 SF OR 0.08AC 5069 (47) 82.62'
S88°56'01"E 38.16' 3,305 SF OR 0.08AC 5067 (46) 82.62'
S88°56'01"E 3,390 SF OR 0.08AC 5065 (45) 82.61'
S88°56'01"E 85.00'
136.00' 42.00' 42.00'
S01°03'59"W 164.00'
C90 C73 C74 L30 L33 L32 L31 77.17' 93.94'

N88°38'38"E 3,720 SF OR 0.09AC 5061 (44) 84.17'
N88°38'38"E 3,293 SF OR 0.08AC 5059 (43) 81.61'
N88°38'38"E 3,326 SF OR 0.08AC 5057 (42) 85.82'
N88°38'38"E 3,773 SF OR 0.09AC 5055 (41) 93.49'
S01°21'22"E 164.00'
C72 C89 C71 C70 C68 C69 C67 C66 29.43' 33.99' C65 C64 C63 11.69' 8.35' 92.79'
S01°03'59"W 63.43'
S01°10'39"E 164.00'
N88°49'21"E 86.84'
N88°49'21"E 85.64' 3,630 SF OR 0.08AC 5049 (40)
N88°49'21"E 84.13' 3,394 SF OR 0.08AC 5047 (39)
N88°49'21"E 85.80' 3,382 SF OR 0.08AC 5045 (38)
N88°49'21"E 3,734 SF OR 0.09AC 5043 (37)
42.00' 40.00' 40.00' 42.00'

S12°36'54"E 42.02' 5039 (33) 3,614 SF OR 0.08AC 42.00'
40.02' 5037 (32) 3,483 SF OR 0.08AC 40.00'
17.81' C62 5035 (31) 3,537 SF OR 0.08AC 40.00'
C61 12.61' 5033 (30) 3,623 SF OR 0.08AC 42.00'
S79°11'25"W 87.96'
S79°11'25"W 85.33'
S79°11'25"W 83.35'
22.36' 87.05'
S10°48'35"E 164.00'
N88°38'38"E 100.38'
C86 C87
COMMON OPEN SPACE LOT 87
AREA ON SHT #4 =
47,602 S.F.
OR 1.093 ACRES

L44 L45

30' PERIMETER PROTECTIVE YARD (SEE NOTE #14)

N01°37'40"E 416.61' 321.75' N 01°58'04"E 1,023.18' (TOTAL)

N90°00'00"W 100.38'

N/F
STANLEY & ELIZABETH TRUSTMAN
PIN 0796-44-1754
ZONED R-4
USE: SF-RESIDENTIAL

N/F
ROBERT A. & JACQUILINE RICHMAN
PIN 0796-44-1641
ZONED R-4
USE: SF-RESIDENTIAL

N/F
FARMER S. SMITH
PIN 0796-44-1449
ZONED R-4
USE: SF-RESIDENTIAL

N/F
ROSALIE J. WHITTINGTON
PIN 0796-44-1345
ZONED R-4
USE: SF-RESIDENTIAL

N/F
RONALD JR. & KATHERINE WHALEY
PIN 0796-44-1232
ZONED R-4
USE: SF-RESIDENTIAL

N/F
JAMES E. & ELIZABETH MORTON
PIN 0796-44-1150
ZONED R-4
USE: SF-RESIDENTIAL

N/F
BEULAH P. PEEK
PIN 0796-43-1948
ZONED R-4
USE: SF-RESIDENTIAL

MATCHLINE SHEET 5 SHEET 4
MATCHLINE SHEET 4 SHEET 3


WAKE COUNTY, NC 343
LAURA M RIDDICK
REGISTER OF DEEDS
PRESENTED & RECORDED ON
08/24/2005 AT 13:34:16
BOOK:BM2005 PAGE:01708

FLOOD PLAIN ORDINANCE
[ ] FEMA MAPPED AREA MAP NUMBER: _____
[X] OTHER: CITY OF RALEIGH FLOOD STUDY 555

APPROVED BY: [signature] 24AUG05

REV: #3 CITY OF RALEIGH REVIEW COMMENTS OF AUGUST 17, 2005
REV: #2 CITY OF RALEIGH REVIEW COMMENTS OF JULY 12, 2005
REV: #1 CITY OF RALEIGH REVIEW COMMENTS

S-40-04
SUBDIVISION
SHEET 4 OF 10
RAO 36 376

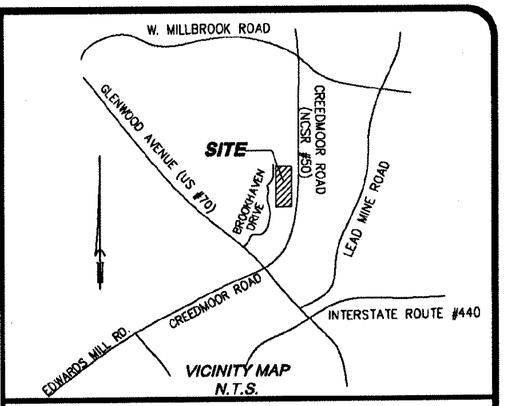

VICINITY MAP
N.T.S.

I, MARK J. OROPALLO, PLS NO. L-4188, CERTIFY TO THE FOLLOWING:

THE SURVEY CREATES A SUBDIVISION OF LAND WITHIN THE AREA OF A COUNTY OR MUNICIPALITY THAT HAS AN ORDINANCE THAT REGULATES PARCELS OF LAND.

I, MARK J. OROPALLO, PLS NO. L-4188, CERTIFY THAT THIS MAP WAS DRAWN FROM AN ACTUAL SURVEY MADE UNDER MY SUPERVISION; THAT THE DEED DESCRIPTION(S) AND PLAT(S) FOR THIS PROPERTY IS (ARE) LISTED HEREON UNDER "REFERENCES"; THAT THE BOUNDARIES NOT SURVEYED ARE CLEARLY INDICATED IN A BROKEN LINETYPE, AND ARE DRAWN FROM INFORMATION SOURCES LISTED UNDER "REFERENCES"; THAT THE RATIO OF PRECISION AS CALCULATED IS 1:10000 OR GREATER, THAT THIS MAP WAS PREPARED IN ACCORDANCE WITH G.S.47-30 AS AMENDED. WITNESSED BY MY ORIGINAL SIGNATURE, LICENSE NUMBER AND SEAL THIS 17TH. DAY OF AUGUST, 2005.

NORTH CAROLINA PROFESSIONAL SEAL L-4188 LAND SURVEYOR MARK J. OROPALLO

MARK J. OROPALLO, PLS
PROFESSIONAL LAND SURVEYOR LIC. # L-4188

DB 11199,	PG. 918	BOM 1952	PG. 94
DB 1112,	PG. 559	BOM 1992,	PG. 855
DB 2796,	PG. 475	BOM 1987,	PG. 480
DB 4114,	PG. 452	BOM 1980,	PG. 548
DB 4114,	PG. 446	BOM 1955,	PG. 110
DB 10708,	PG. 9	BOM 1978,	PG. 443
DB 1556,	PG. 107	BOM 1959,	PG. 227
DB 1631,	PG. 469	BOM 1998,	PG. 1824
		BOM 1999,	PG. 1412

OWNERS ADDRESS:
PULTE HOME CORPORATION
801 CORPORATE CENTER DRIVE
SUITE 118, RALEIGH N.C. 27607

PIN 0796-44-4054 0796-45-1061
0796-44-4876 0796-45-2245

TAX MAP # 0796.14

DRAWN BY: D.S.Z.

CHECKED BY: K.S.

LEGEND:

- EXISTING IRON PIPE
- IRON PIN SET
- MATHEMATICAL POINT
- EXISTING N.C. DOT R/W DISK
- NORTH CAROLINA RIGHT-OF-WAY CONCRETE MONUMENT
- CONTROL CORNER
- IPS IRON PIN SET
- 50' NEUSE RIVER BUFFER LINE
- 0000 STREET ADDRESS
- N.C.G.S. CONTROL MONUMENT
- DB DEED BOOK
- PG PAGE
- BOM BOOK OF MAPS
- EIR EXISTING IRON ROD
- R/W RIGHT OF WAY
- 50' NATURAL PROTECTIVE YARD
- 100 YEAR FLOOD PLAIN
- C.O.R. CITY OF RALEIGH
- EXISTING 20' & 10' C.O.R. SANITARY SEWER AND WATER LINE EASEMENTS HEREBY ABANDONED PER CITY COUNCIL RESOLUTION NUMBER 2005-595.
- NEW CITY OF RALEIGH WATER AND SEWER EASEMENT HEREBY DEDICATED

Book 2005 pg 1708

REVISIONS
#1 6/08/2005
#2 7/25/2005
#3 8/17/2005

SUBDIVISION PLAT AND RIGHT OF WAY DEDICATION FOR "COPPER RIDGE TOWNHOMES"

CITY:	COUNTY:	STATE:	DATE:	DRAWING:
RALEIGH	WAKE	NORTH CAROLINA	APRIL 28, 2005	99-08-16

SURVEYED by

MSS LAND CONSULTANTS
5540 McNeely Dr.
(Suite 101)
Raleigh, NC 27612
Phone (919) 510-4464
Fax (919) 510-9102
Email: oropallomj@mssland.com

"Committed to Total Quality Service"

O:/PULTE/99-08-16/DWG/COPPERSUBD.DWG

O:_PULTE\99-08-16\dwg\copperrsubd.DWG, layout, 08/17/2005 04:44:15 PM, smeel