THIS PLAT IS A CORRECT REPRESENTATION OF THE LANDS SURVEYED; HOWEVER A NORTH CAROLINA LICENSED ATTORNEY SHOULD BE CONSULTED CONCERNING CORRECT OWNERSHIP, WIDTH AND LOCATION OF ANY EASEMENTS, ANY CEMETERIES, OR FAMILY BURIAL GROUNDS NOT SHOWN ON RECORDED MAPS OR DEEDS MADE AVAILABLE TO THIS SURVEYOR BY THE RECENT OWNERS AT THE TIME OF THIS SURVEY AND OTHER TITLE QUESTIONS REVEALED BY TITLE EXAMINATION. NO RESPONSIBILITY OF ANY NATURE IS ASSUMED BY THIS SURVEYOR FOR ANY CONDITIONS WHICH MAY EXIST BUT ARE UNKN [redacted] *GROUNDS, TOXIC OR* [redacted] *TANKS, ETC.*

CERTIFICATION OF OWNERSHIP AND DEDICATION

I HEREBY CERTIFY THAT I AM THE OWNER OF THE PROPERTY SHOWN AND DESCRIBED HEREON, WHICH [redacted]

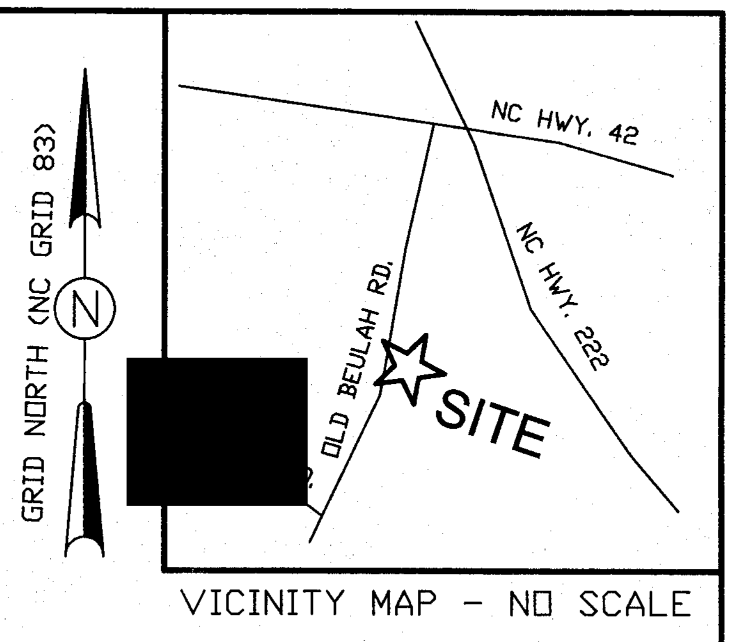

VICINITY MAP - NO SCALE

GRID NORTH (NC GRID 83)
N
NC HWY. 42
NC HWY. 222
OLD BEULAH RD.
SITE

[redacted]

LEGEND

N&C	NAIL AND CAP
PKS	PK NAIL SET
EIP	EXISTING IRON PIPE
EIS	EXISTING IRON STAKE
IPS	IRON PIPE SET
PUP	POINT UNDER PAVEMENT
R/W	RIGHT-OF-WAY
CL	CENTERLINE

REF: BEING A RECOMBINATION OF A PORTION OF TRACT FOUR SHOWN IN D.B. 3028, PG. 690 WITH THE A [redacted] PERTY SHOWN IN DEED BOK 814, PG. 800 OF THE [redacted] COUNTY REGISTER OF DEEDS OFFICE.

PLAT REFERENCES: PB 61, PG. 57
PB 55, PG. 339
PB 78, PG. 242
PB 93, PG. 229

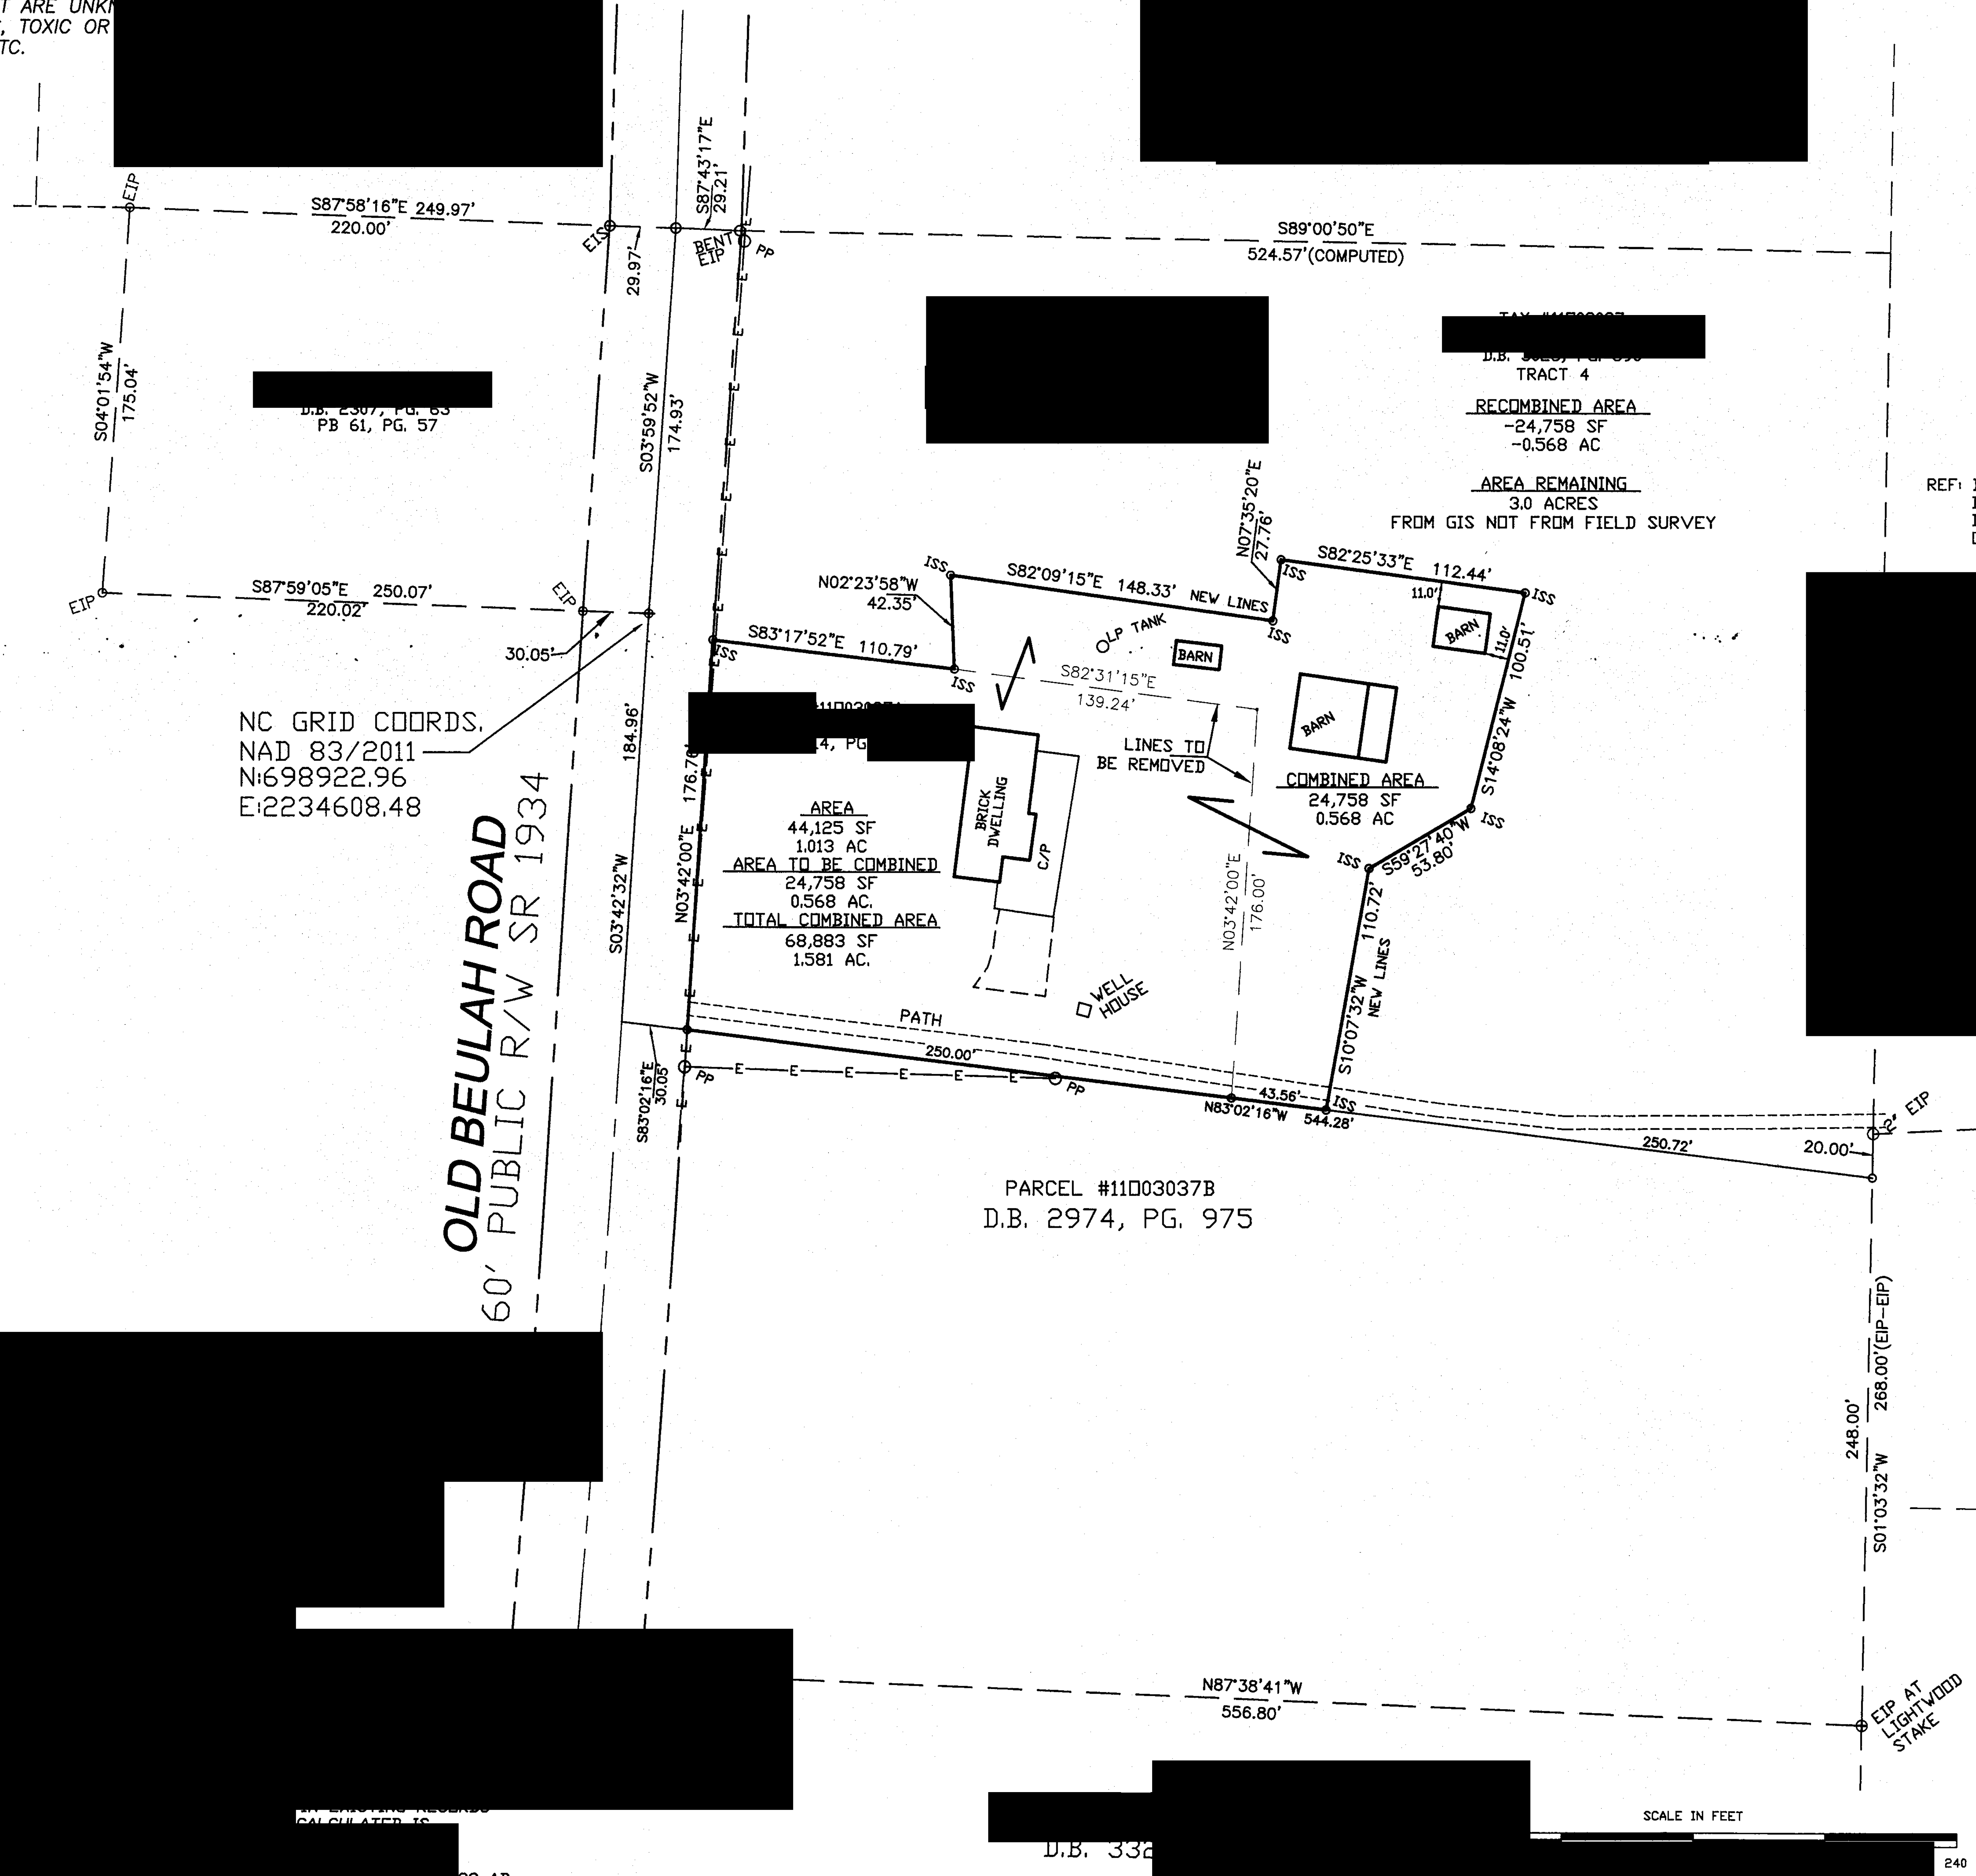

EIP
S87°58'16"E 249.97'
220.00'
EIS
29.97'
S87°43'17"E
29.21'
BENT EIP
PP
S89°00'50"E
524.57'(COMPUTED)
S04°01'54"W
175.04'
[redacted]
PB 61, PG. 57
S03°59'52"W
174.93'
[redacted]
[redacted]
TRACT 4
RECOMBINED AREA
-24,758 SF
-0.568 AC
AREA REMAINING
3.0 ACRES
FROM GIS NOT FROM FIELD SURVEY
EIP
S87°59'05"E 250.07'
220.02'
EIP
30.05'
NC GRID COORDS.
NAD 83/2011
N:698922.96
E:2234608.48
184.96'
N02°23'58"W
42.35'
ISS
S82°09'15"E 148.33' NEW LINES
N07°35'20"E
27.76'
S82°25'33"E 112.44'
11.0'
BARN
11.0'
100.51'
S83°17'52"E 110.79'
LP TANK
BARN
S82°31'15"E
139.24'
[redacted]
LINES TO BE REMOVED
BARN
COMBINED AREA
24,758 SF
0.568 AC
S14°08'24"W
S59°27'40"W
53.80'
176.7
N03°42'00"E
AREA
44,125 SF
1.013 AC
AREA TO BE COMBINED
24,758 SF
0.568 AC.
TOTAL COMBINED AREA
68,883 SF
1.581 AC.
BRICK DWELLING
C/P
N03°42'00"E
176.00'
110.72'
S10°07'32"W
NEW LINES
WELL HOUSE
PATH
S03°42'32"W
OLD BEULAH ROAD
60' PUBLIC R/W SR 1934
250.00'
S83°02'16"E
30.05'
PP
E
43.56'
N83°02'16"W
544.28'
250.72'
20.00'
2" EIP
PARCEL #11003037B
D.B. 2974, PG. 975
248.00'
268.00'(EIP-EIP)
S01°03'32"W
N87°38'41"W
556.80'
EIP AT LIGHTWOOD STAKE
D.B. 332
[redacted]
SCALE IN FEET
240

[redacted]

23 AD.

Filed i [redacted]
Filed [redacted] 023 10:36:12 AM
[redacted] Register of Deeds
Dep/Asst Ineal
PLAT B: 99 P: 190

[redacted]

MENTS FOR RECORDING [redacted]

9-8-2023
DATE

OWNER: [redacted]
10720 OLD BEULAH RD.
KENLY, NC

CORP. #L-3000

PC

RECOMBINATION SURVEY FOR

[redacted]

AJB

[redacted] AYNE