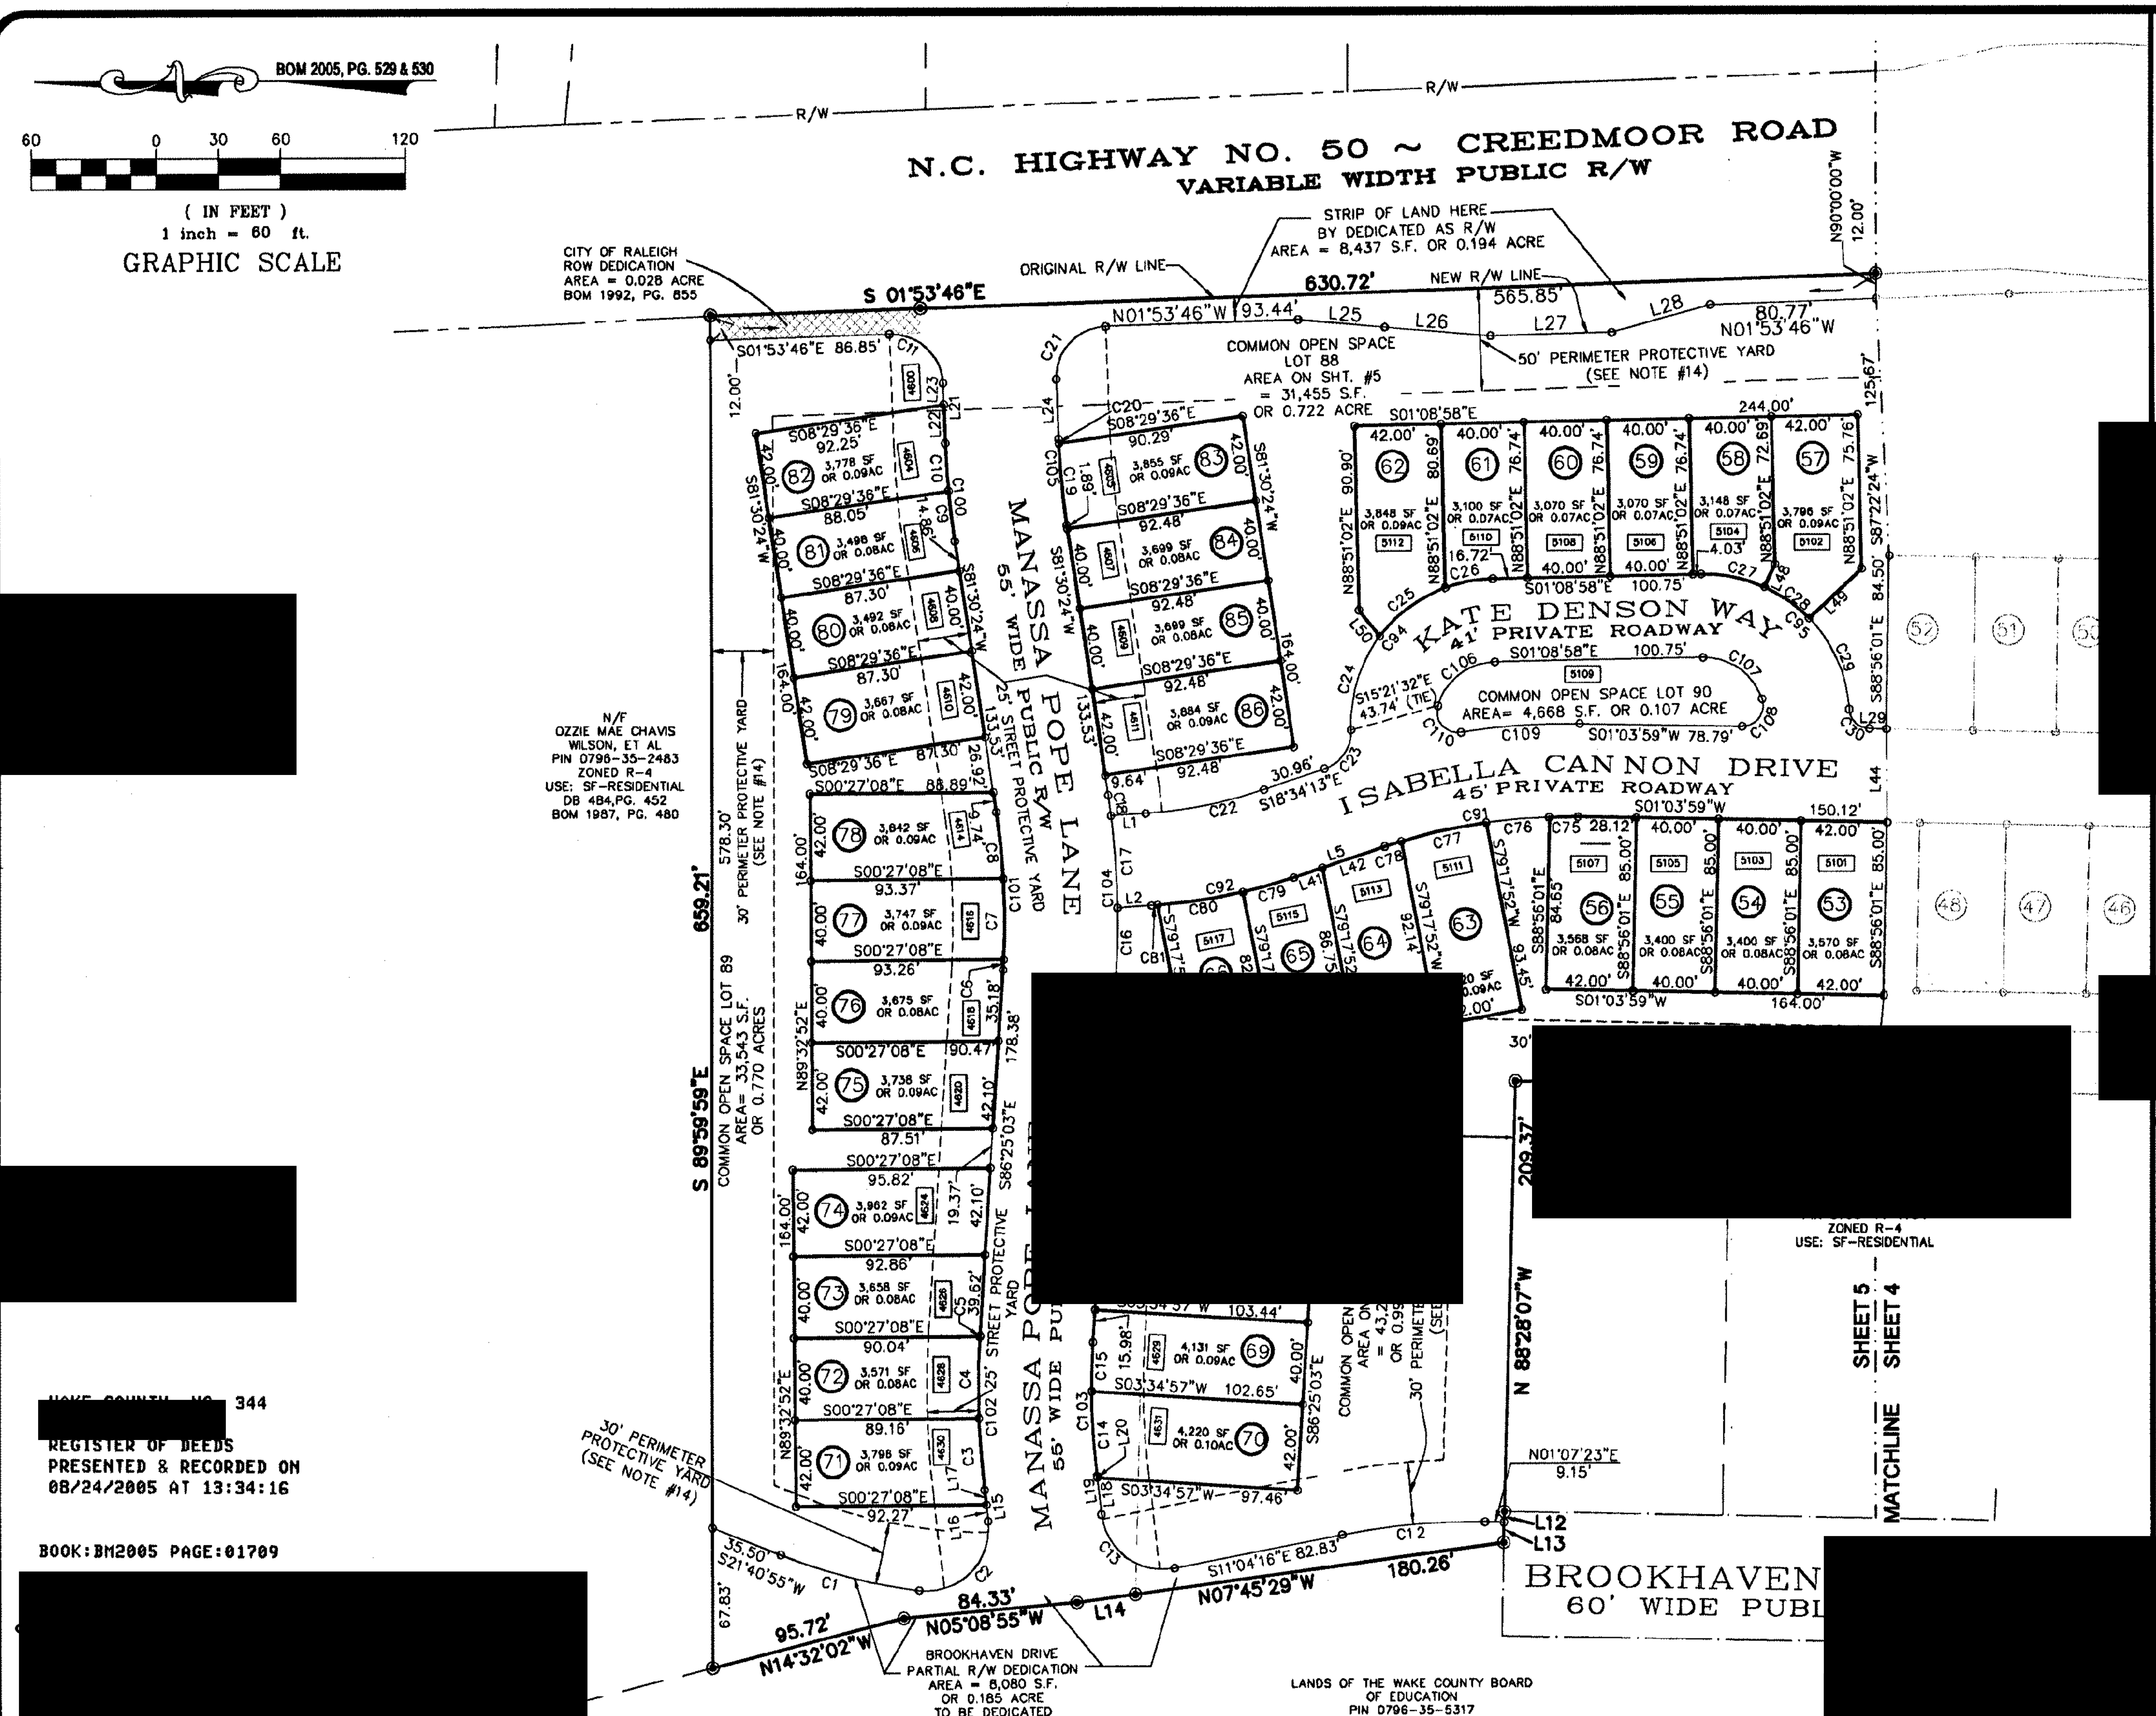

[redacted]

[redacted]

[redacted]

[redacted]

[redacted]

[redacted]

LANDS OF THE WAKE COUNTY BOARD OF EDUCATION
PIN 0796-35-5317
ZONED R-4 USE: SCHOOL
DB 1613, PG. 649
DB 1556, PG. 107
DB 2796, PG. 475

REV: #3 CITY OF RALEIGH REVIEW COMMENTS OF AUGUST 17, 2005
REV: #2 CITY OF RALEIGH REVIEW COMMENTS OF JULY 12, 2005
REV: #1 CITY OF RALEIGH REVIEW COMMENTS

[redacted] 344
REGISTER OF DEEDS
PRESENTED & RECORDED ON
08/24/2005 AT 13:34:16

BOOK:BM2005 PAGE:01709

[redacted]

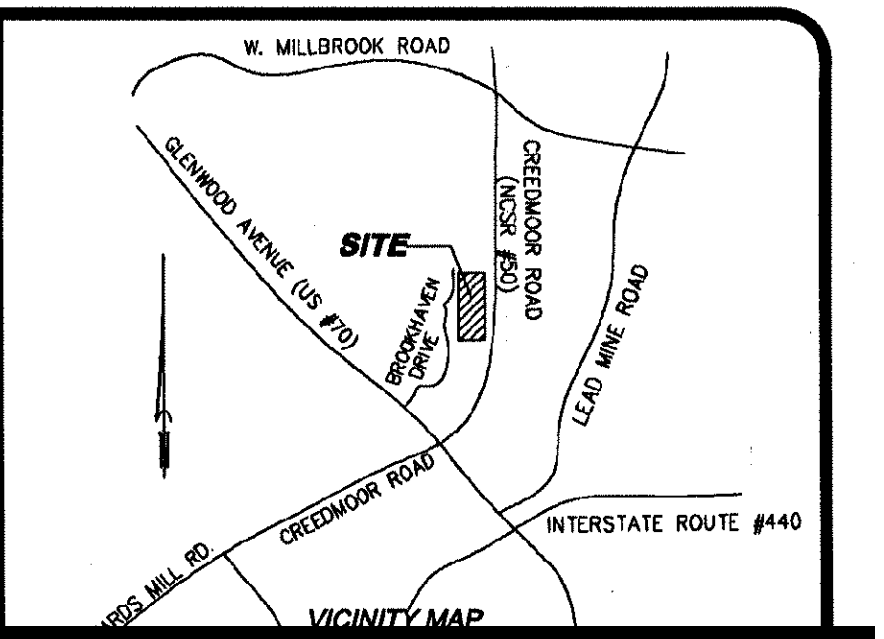

[redacted]

REFERENCES

DB 11199,	PG. 918	BOM 1952	PG. 94		
DB 1112,	PG. 559	BOM 1992,	PG. 855		
DB 2796,	PG. 475	BOM 1987,	PG. 480		
DB 4114,	PG. 452	BOM 1980,	PG. 548		
DB 4114,	PG. 446	BOM 1955,	PG. 110		
DB 10708,	PG. 9	BOM 1978,	PG. 443		
DB 1556,	PG. 107	BOM 1959,	PG. 227		
DB 1631,	PG. 469	BOM 1998,	PG. 1824		
		BOM 1999,	PG. 1412		

LEGEND:

◉	EXISTING IRON PIPE
○	IRON PIN SET
△	MATHEMATICAL POINT
⊡	EXISTING N.C. DOT R/W DISK
■	NORTH CAROLINA RIGHT-OF-WAY CONCRETE MONUMENT
◎	CONTROL CORNER
IPS	IRON PIN SET
▒	50' NEUSE RIVER BUFFER LINE
0000	STREET ADDRESS
▲	N.C.G.S. CONTROL MONUMENT
DB	DEED BOOK
PG	PAGE
BOM	BOOK OF MAPS
EIR	EXISTING IRON ROD
R/W	RIGHT OF WAY
▨	50' NATURAL PROTECTIVE YARD
▧	100 YEAR FLOOD PLAIN
C.O.R.	CITY OF RALEIGH
▩	EXISTING 20' & 10' C.O.R. SANITARY SEWER AND WATER LINE EASEMENTS HEREBY ABANDONED PER CITY COUNCIL RESOLUTION NUMBER 2005-595.
▨	NEW CITY OF RALEIGH WATER EASEMENT HEREBY DEDICATED

REVISIONS
#1 6/08/2005
#2 7/25/2005
#3 8/17/2005

SUBDIVISION PLAT
RIGHT OF WAY DEDICATION
FOR
"COPPER RIDGE TOWNHOME

[redacted]

CITY:	COUNTY:	STATE:	DATE:	DRAW
RALEIGH	WAKE	NORTH CAROLINA	APRIL 28, 2005	99-08-16