[redacted]

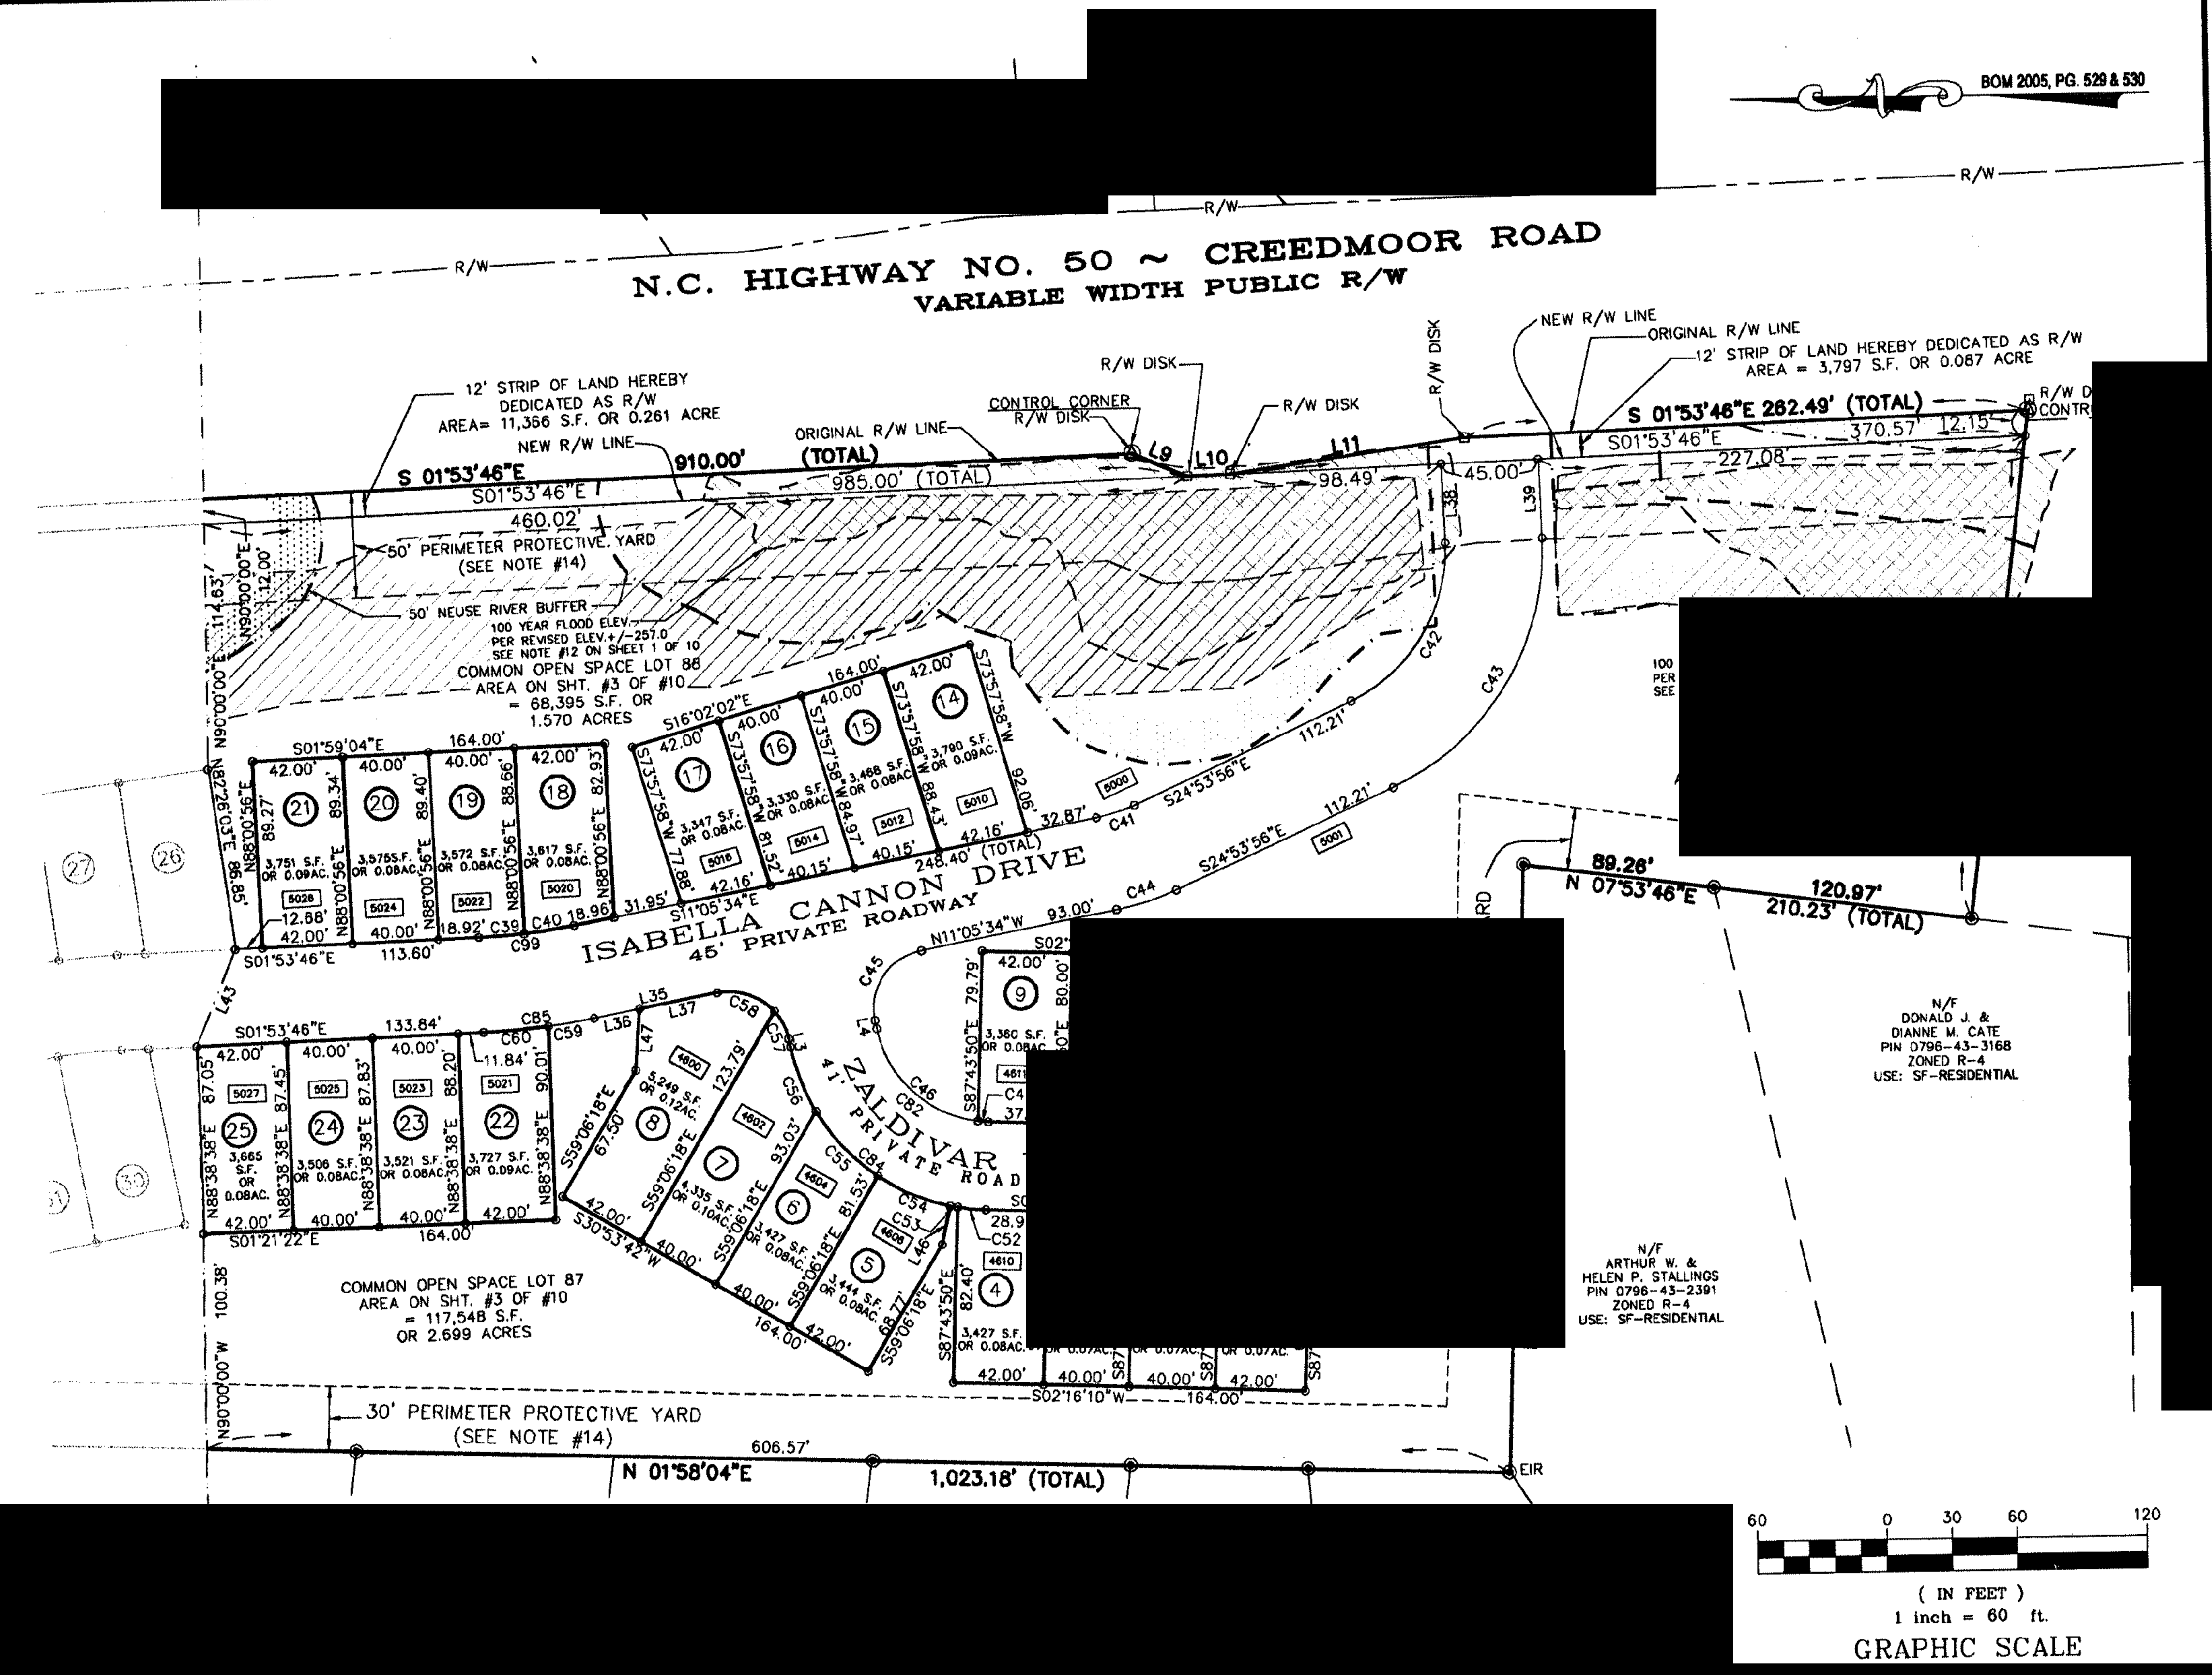
BOM 2005, PG. 529 & 530
R/W
N.C. HIGHWAY NO. 50 ~ CREEDMOOR ROAD
VARIABLE WIDTH PUBLIC R/W
12' STRIP OF LAND HEREBY DEDICATED AS R/W AREA= 11,356 S.F. OR 0.261 ACRE
NEW R/W LINE
ORIGINAL R/W LINE
CONTROL CORNER R/W DISK
R/W DISK
S 01°53'46"E 910.00' (TOTAL)
S01°53'46"E 985.00' (TOTAL)
460.02'
98.49'
45.00'
L9
L10
L11
L38
L39
NEW R/W LINE
ORIGINAL R/W LINE
12' STRIP OF LAND HEREBY DEDICATED AS R/W AREA = 3,797 S.F. OR 0.087 ACRE
S 01°53'46"E 282.49' (TOTAL)
S01°53'46"E
370.57'
12.15'
227.08'
50' PERIMETER PROTECTIVE YARD (SEE NOTE #14)
50' NEUSE RIVER BUFFER
100 YEAR FLOOD ELEV. PER REVISED ELEV.+/-257.0 SEE NOTE #12 ON SHEET 1 OF 10
COMMON OPEN SPACE LOT 88 AREA ON SHT. #3 OF #10 = 68,395 S.F. OR 1.570 ACRES
N90°00'00"E 114.63'
12.00'
N90°00'00"E
ISABELLA CANNON DRIVE
45' PRIVATE ROADWAY
ZALDIVAR
41' PRIVATE ROAD
S24°53'56"E 112.21'
S24°53'56"E 112.21'
S11°05'34"E
N11°05'34"W 93.00'
248.40' (TOTAL)
32.87'
S01°59'04"E 164.00'
S16°02'02"E
164.00'
N88°22'03"E 96.85'
S01°53'46"E 113.60'
12.88'
S01°53'46"E 133.84'
S01°21'22"E 164.00'
S30°53'42"W
S02°16'10"W 164.00'
COMMON OPEN SPACE LOT 87 AREA ON SHT. #3 OF #10 = 117,548 S.F. OR 2.699 ACRES
N00°00'00"W 100.38'
30' PERIMETER PROTECTIVE YARD (SEE NOTE #14)
606.57'
N 01°58'04"E 1,023.18' (TOTAL)
EIR
89.26'
N 07°53'46"E
120.97'
210.23' (TOTAL)
N/F DONALD J. & DIANNE M. CATE PIN 0796-43-3168 ZONED R-4 USE: SF-RESIDENTIAL
N/F ARTHUR W. & HELEN P. STALLINGS PIN 0796-43-2391 ZONED R-4 USE: SF-RESIDENTIAL
21 3,751 S.F. OR 0.09AC. 5028
20 3,575 S.F. OR 0.08AC. 5024
19 3,572 S.F. OR 0.08AC. 5022
18 3,617 S.F. OR 0.08AC. 5020
17 3,347 S.F. OR 0.08AC. 5016
16 3,330 S.F. OR 0.08AC. 5014
15 3,468 S.F. OR 0.08AC. 5012
14 3,790 S.F. OR 0.09AC. 5010
25 3,665 S.F. OR 0.08AC. 5027
24 3,506 S.F. OR 0.08AC. 5025
23 3,521 S.F. OR 0.08AC. 5023
22 3,727 S.F. OR 0.09AC. 5021
8 5,249 S.F. OR 0.12AC. 4800
7 4,335 S.F. OR 0.10AC. 4602
6 3,427 S.F. OR 0.08AC. 4604
5 3,444 S.F. OR 0.08AC. 4608
4 3,427 S.F. OR 0.08AC. 4610
9 3,360 S.F. OR 0.08AC.
5000
5001
27
26
30
60 0 30 60 120
(IN FEET)
1 inch = 60 ft.
GRAPHIC SCALE

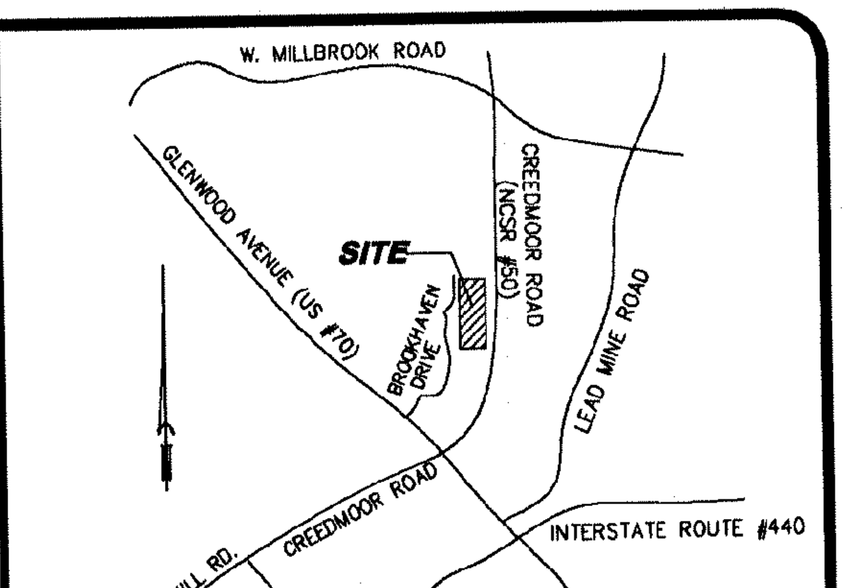
W. MILLBROOK ROAD
GLENWOOD AVENUE (US #70)
SITE
BROOKHAVEN DRIVE
CREEDMOOR ROAD (NCSR #50)
LEAD MINE ROAD
CREEDMOOR ROAD
MILL RD.
INTERSTATE ROUTE #440

[redacted]

[redacted]

[redacted]

[redacted]

[redacted]

[redacted]

[redacted]

[redacted]

[redacted]

IPE
POINT
EXISTING N.C. DOT R/W DISK
NORTH CAROLINA RIGHT-OF-WAY CONCRETE MONUMENT
CONTROL CORNER
IPS IRON PIN SET
50' NEUSE RIVER BUFFER LINE

0000 STREET ADDRESS
N.C.G.S. CONTROL MONUMENT
DB DEED BOOK
PG PAGE
BOM BOOK OF MAPS
EIR EXISTING IRON ROD
R/W RIGHT OF WAY
50' NATURAL PROTECTIVE YARD

100 YEAR FLOOD PLAIN
C.O.R. CITY OF RALEIGH
EXISTING 20' & 10' C.O.R SANITARY SEWER AND WATER LINE EASEMENTS HEREBY ABANDONED PER CITY COUNCIL RESOLUTION NUMBER 2005-595
NEW CITY OF RALEIGH WATER EASEMENT HEREBY DEDICATED

#2 7/25/2005
#3 8/17/2005

RIGHT OF WAY DEDICATION FOR "COPPER RIDGE TOWNHOMES"

	COUNTY:	STATE:	DATE:	DRAWING:
RALEIGH	WAKE	NORTH CAROLINA	APRIL 28, 2005	99-08-16

Book 2005 pg 1707

mbd.DWG, layout, 08/17/2005 04:43:02 PM, zmed

[redacted]